


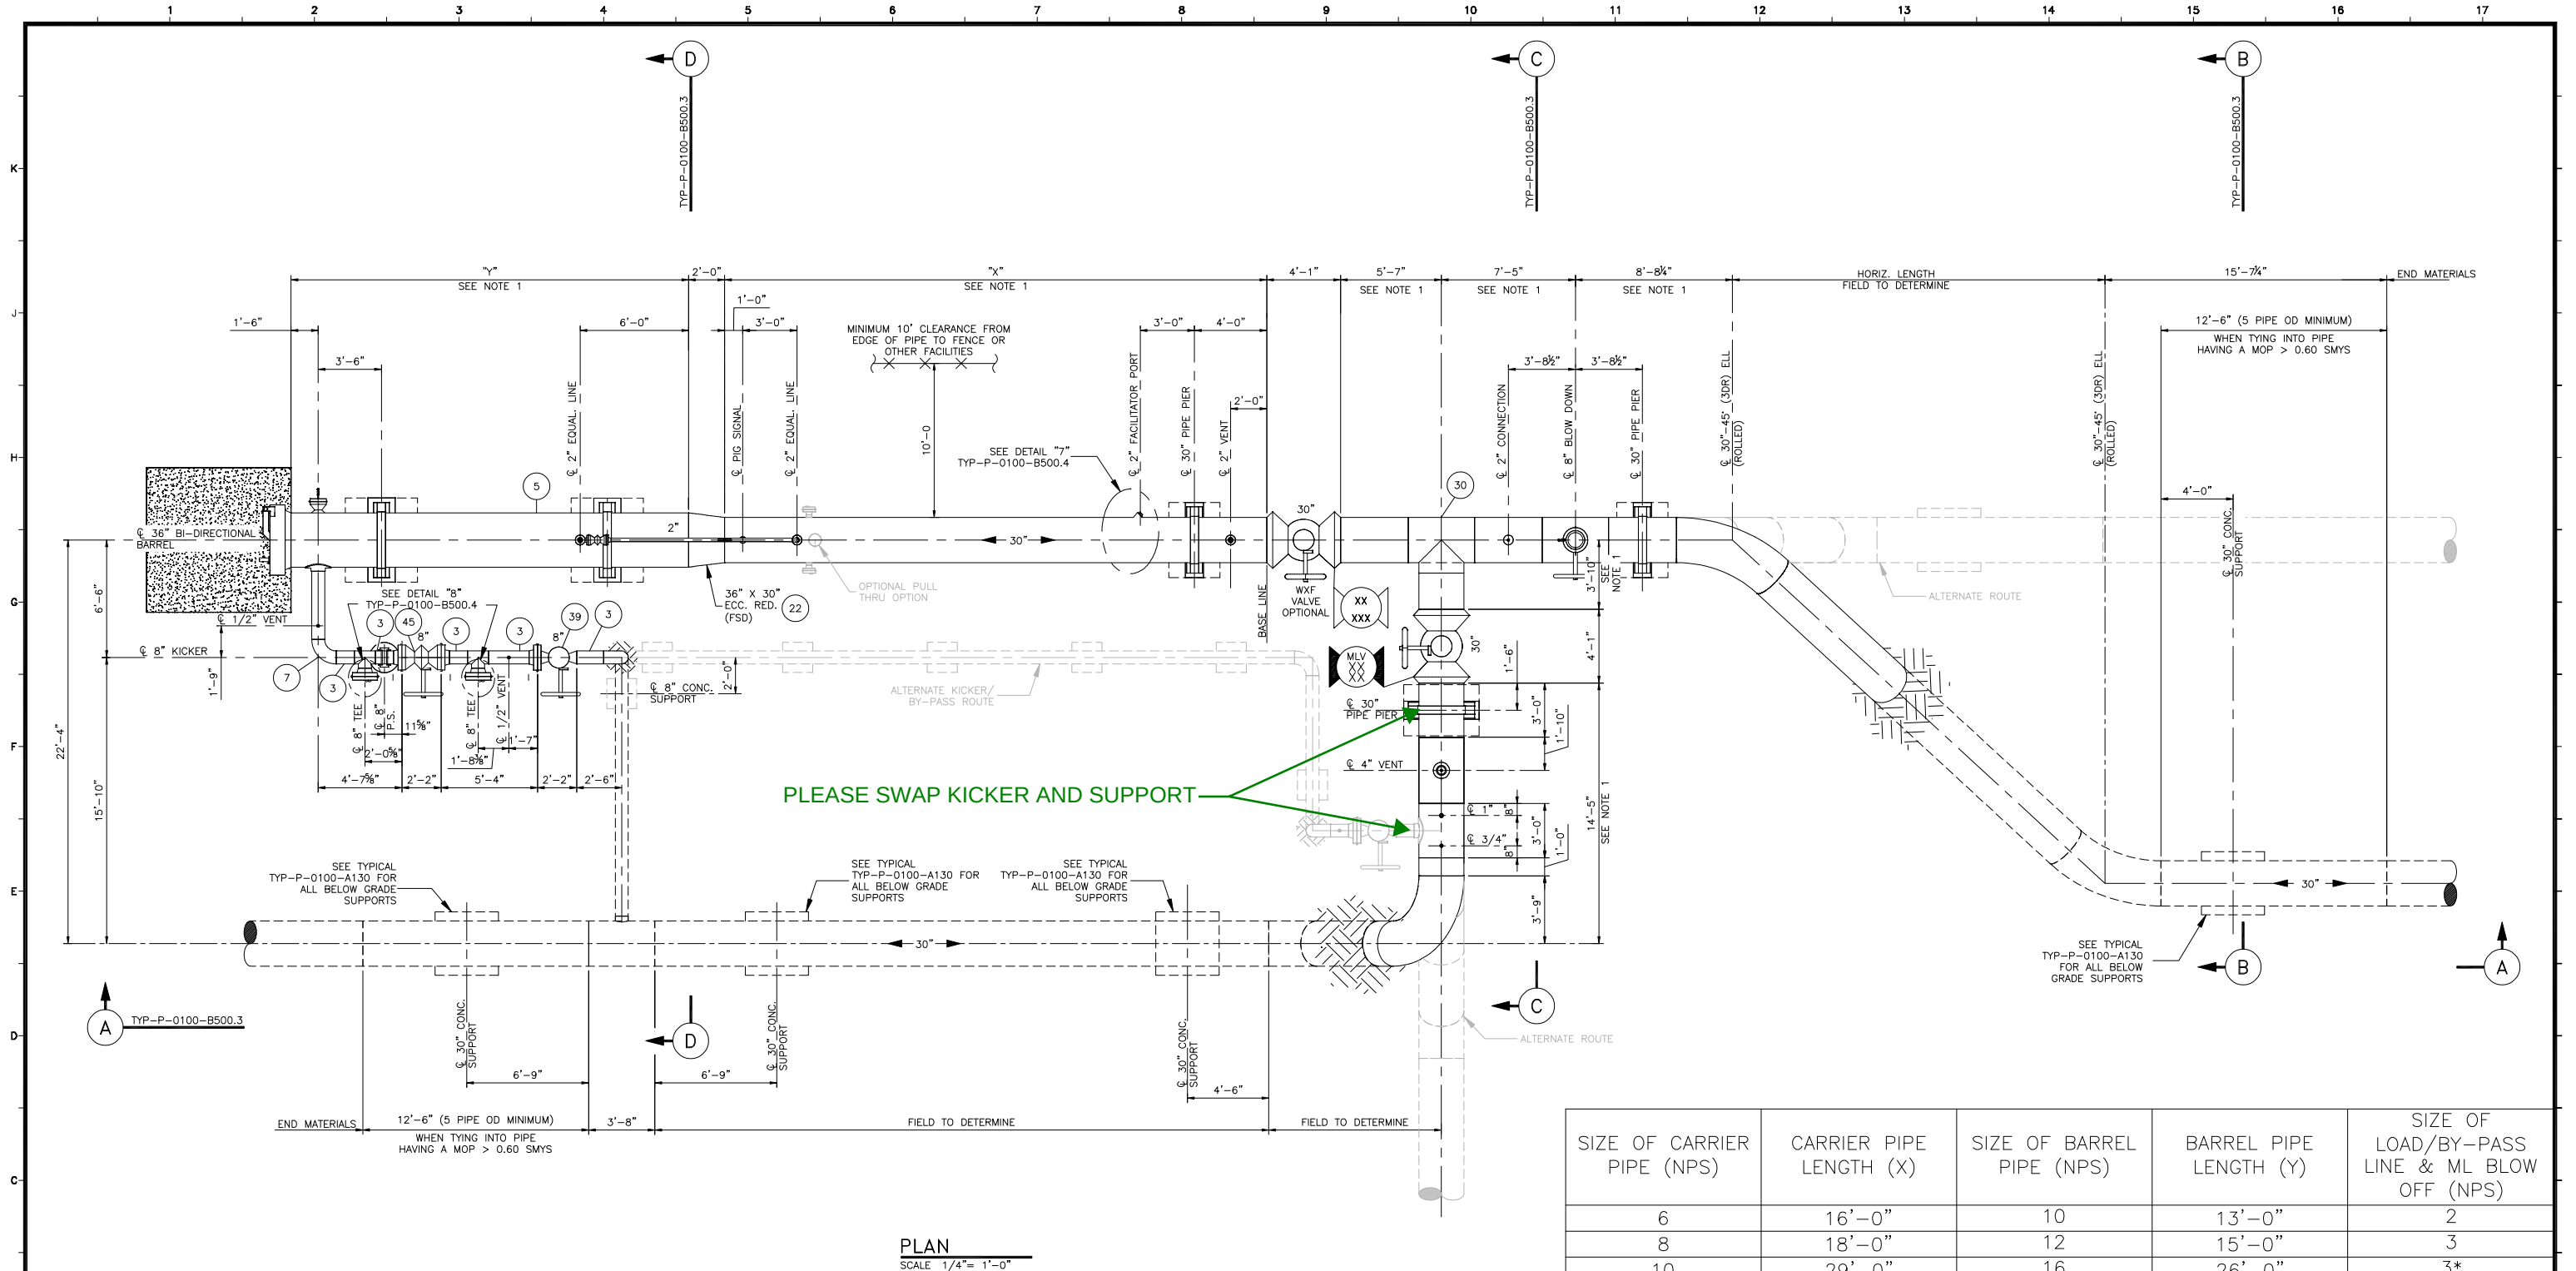

PLAN
SCALE 1/4" = 1'-0"


- NOTES:
1. MINIMUM PIPE LENGTH IS 6"; HOWEVER, 1.5 TIMES PIPE OF LENGTHS ARE PREFERRED IF SPACE ALLOWS.
 2. MINIMUM BLOWDOWN OUTLET HEIGHT TO BE 6'-6" FROM FINISHED GRADE.
 3. ABOVE GRADE HORIZONTAL ELEVATION TO BE 3' TO 3'-6" FROM FINISHED GRADE FOR 3" OR 4" DRAIN VALVE CLEARANCE.
 4. VALVE HAND WHEELS ARE TO BE POSITIONED AS DRAWN.
 5. USE EFFICIENCY MANUAL GEAR OPERATOR ON VALVES 16" > 14". (MAXTORQUE/WEDGEROCK); 36" AND LARGER USE AN ACTUATOR CONVENIENCE OPERATOR.
 6. USE QUICK OPENING HINGED CLOSURES FOR ALL HORIZONTAL CLOSURES; USE FLANGED END, QUICK OPENING HINGED CLOSURES RECOMMENDED FOR ALL THREADED OPENINGS FOR LUGLESS VERTICAL CLOSURES. ALL CLOSURES C/W PAV.
 7. PULL-THROUGH PORT(S) TO BE POSITIONED TO CLEAR OF ANY ENVIRONMENTAL INTERFERENCES. A 12 O'CLOCK POSITION MAY BE REQUIRED OR PREFERRED. SEE TYP-P-0100-A225 OR TYP-P-0100-A226 FOR PULL-THROUGH PORT DESIGN.
 8. FIVE (5) PIPE OUTSIDE DIAMETERS LENGTH OF PIPE IS REQUIRED FROM LAST ASSEMBLY'S FITTING WHEN TYING INTO PIPE WITH A DESIGN FACTOR >0.60.
 9. DIMENSIONS SHOWN HAVE BEEN APPROVED BY KM ENGINEERING. ANY DEVIATIONS OF "X" AND "Y" DIMENSIONS WILL NEED TO BE APPROVED BY KM ENGINEERING.
 10. ONLY 1 BALL VALVE IS NEEDED IN THE KICKER LINE.

SIZE OF CARRIER PIPE (NPS)	CARRIER PIPE LENGTH (X)	SIZE OF BARREL PIPE (NPS)	BARREL PIPE LENGTH (Y)	SIZE OF LOAD/BY-PASS LINE & ML BLOW OFF (NPS)
6	16'-0"	10	13'-0"	2
8	18'-0"	12	15'-0"	3
10	29'-0"	16	26'-0"	3*
12	22'-0"	16	19'-0"	4
16	26'-0"	20	23'-0"	6
20	23'-0"	24	20'-0"	6
22	22'-0"	26	19'-0"	8
24	22'-0"	30	19'-0"	8
26	24'-0"	30	21'-0"	8
30	29'-0"	36	26'-0"	8
36	23'-0"	42	20'-0"	10
42	27'-0"	48	24'-0"	16


* NPS 4 MINIMUM BLOW OFF SIZE RECOMMENDED FOR EASE OF AIR MOVER INSTALLATION.

0 ISSUED FOR ADC APPROVAL		07-18-2022		NOTES: 1) USE KM CADWORX PIPING SPECIFICATIONS THAT MEETS OR EXCEED SYSTEM DESIGN PRESSURE & TEMPERATURE.		KINDERMORGAN		PLAN TYPICAL 30" BI-DIRECTIONAL LAUNCHER/RECEIVER		Status: ISSUED FOR ADC APPROVAL State: PIN No: County: Scale: AS SHOWN Category: DETAIL File Name: TYP-P-0100-B500.1.dwg Drawing No: TYP-P-0100-B500.1 Rev 0	
Revision Description		Project ID		Date							

<

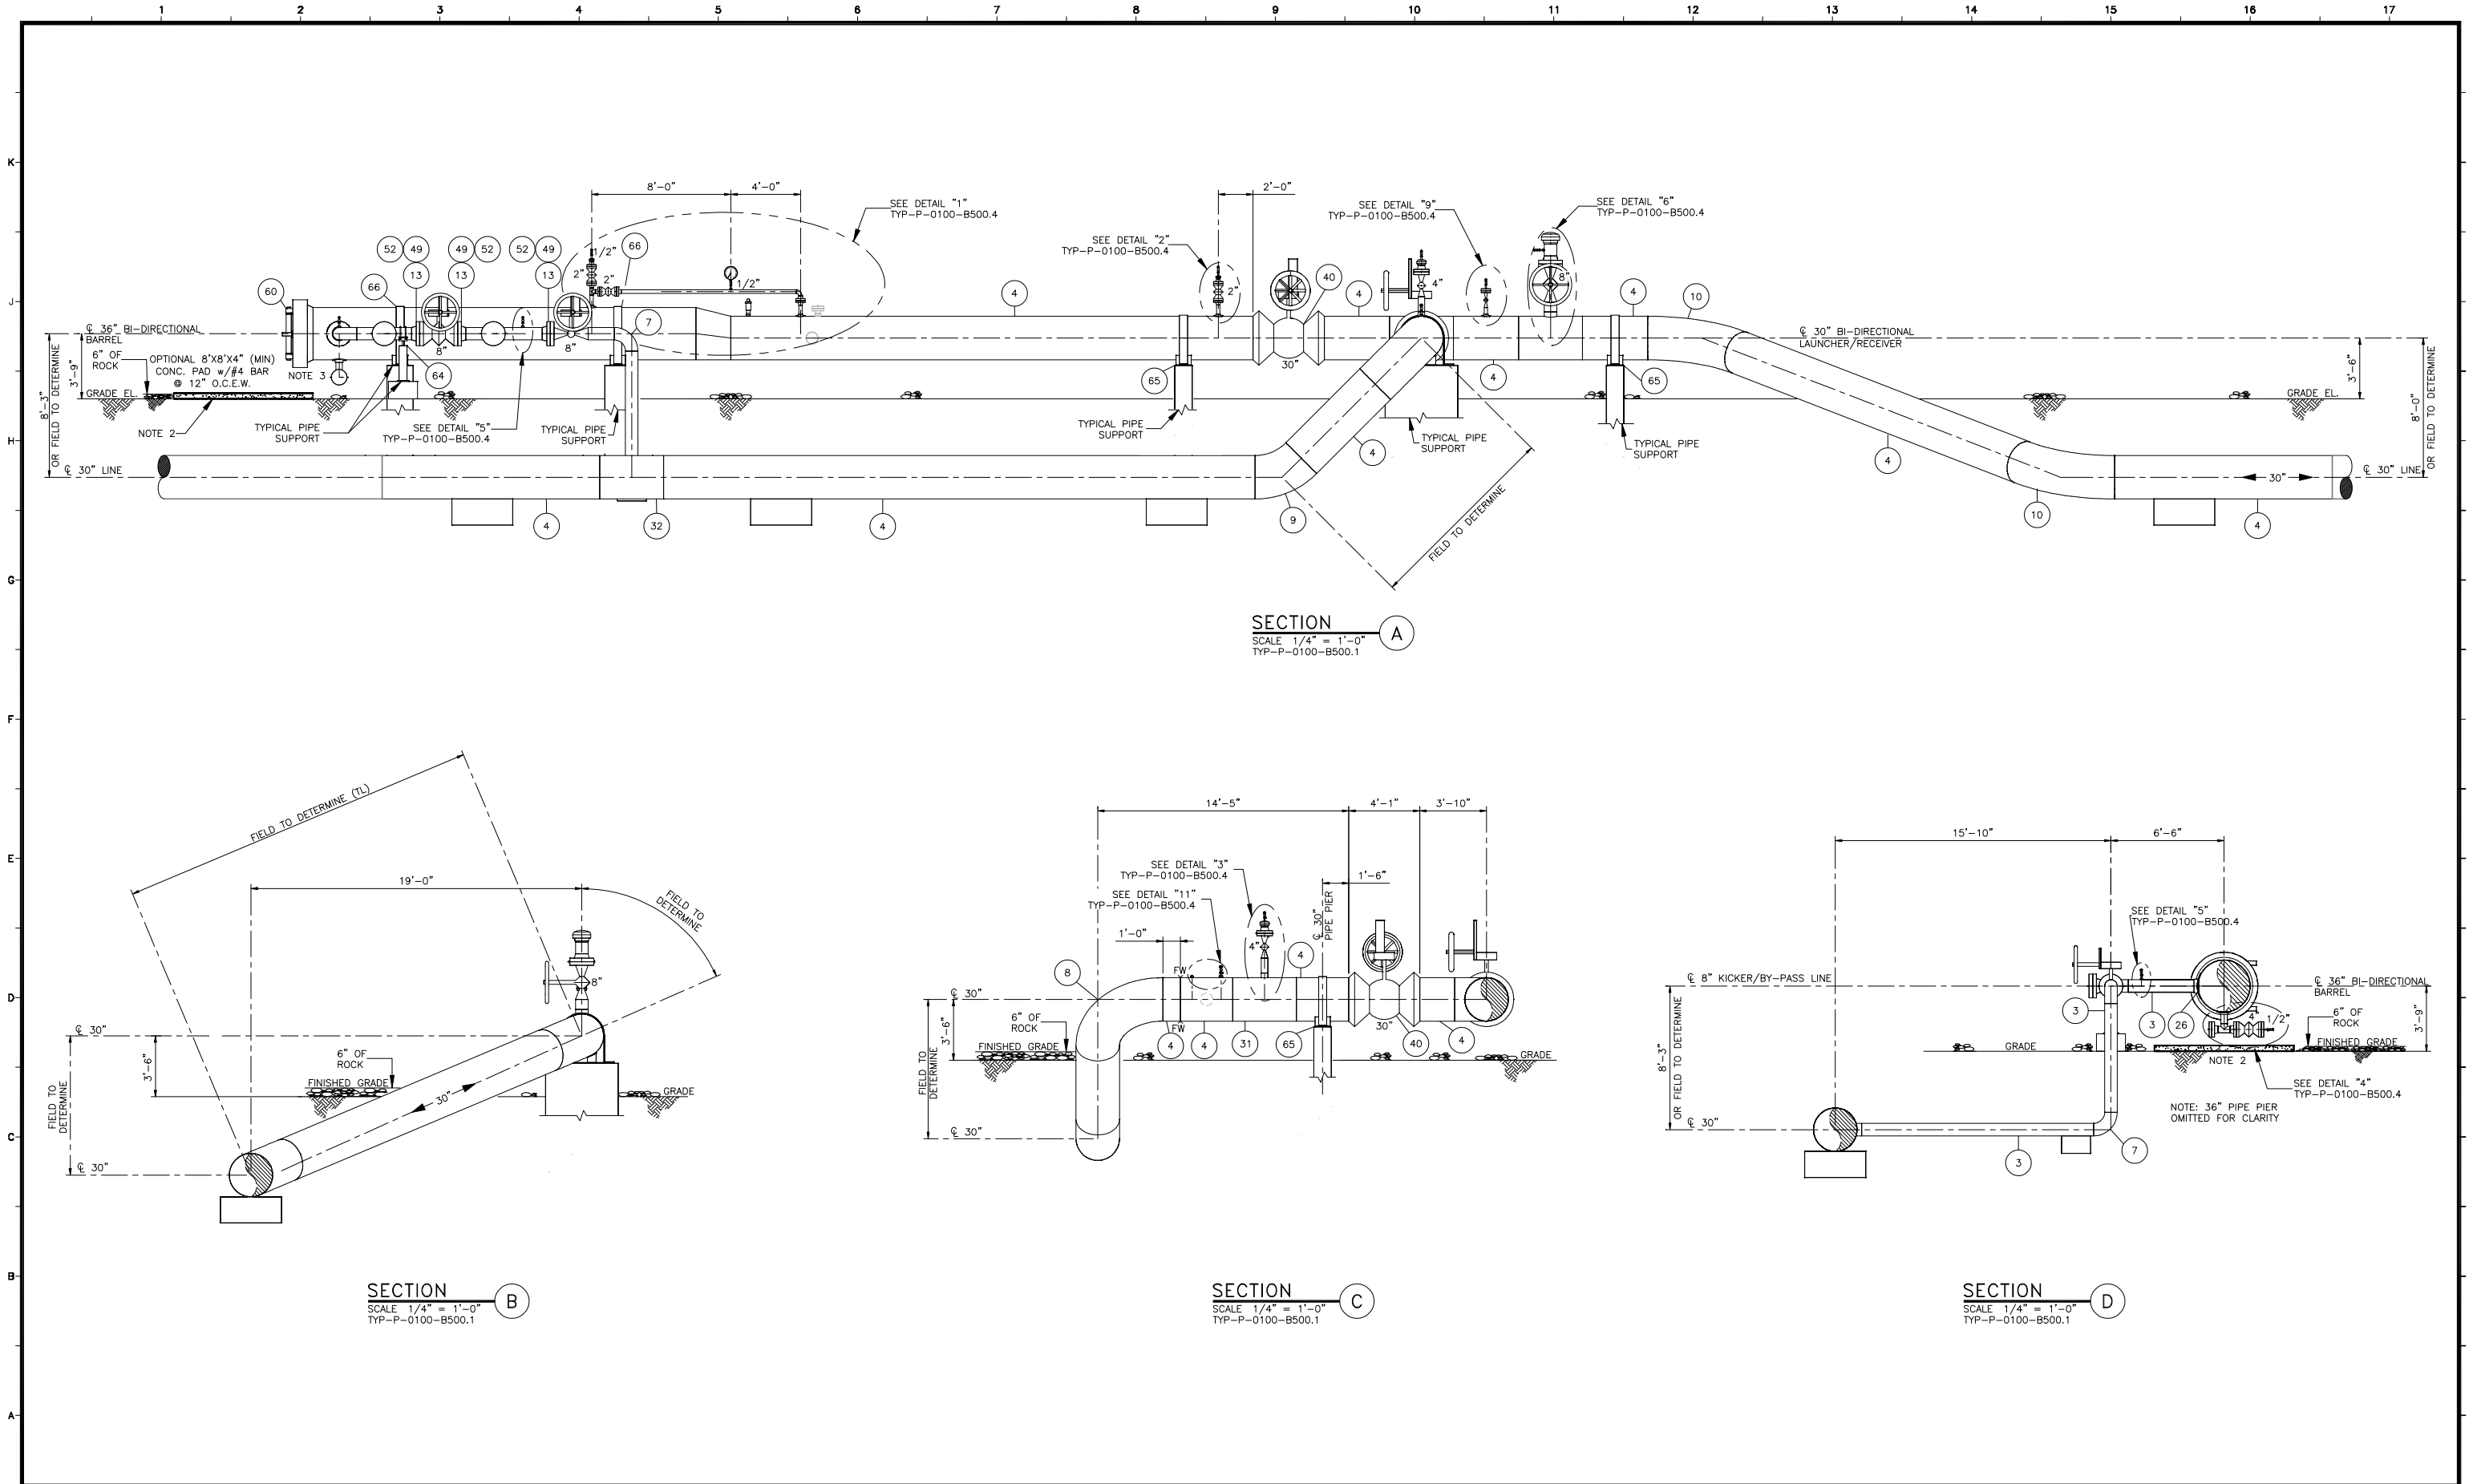

				:Reference Drawings		:Facility Name	

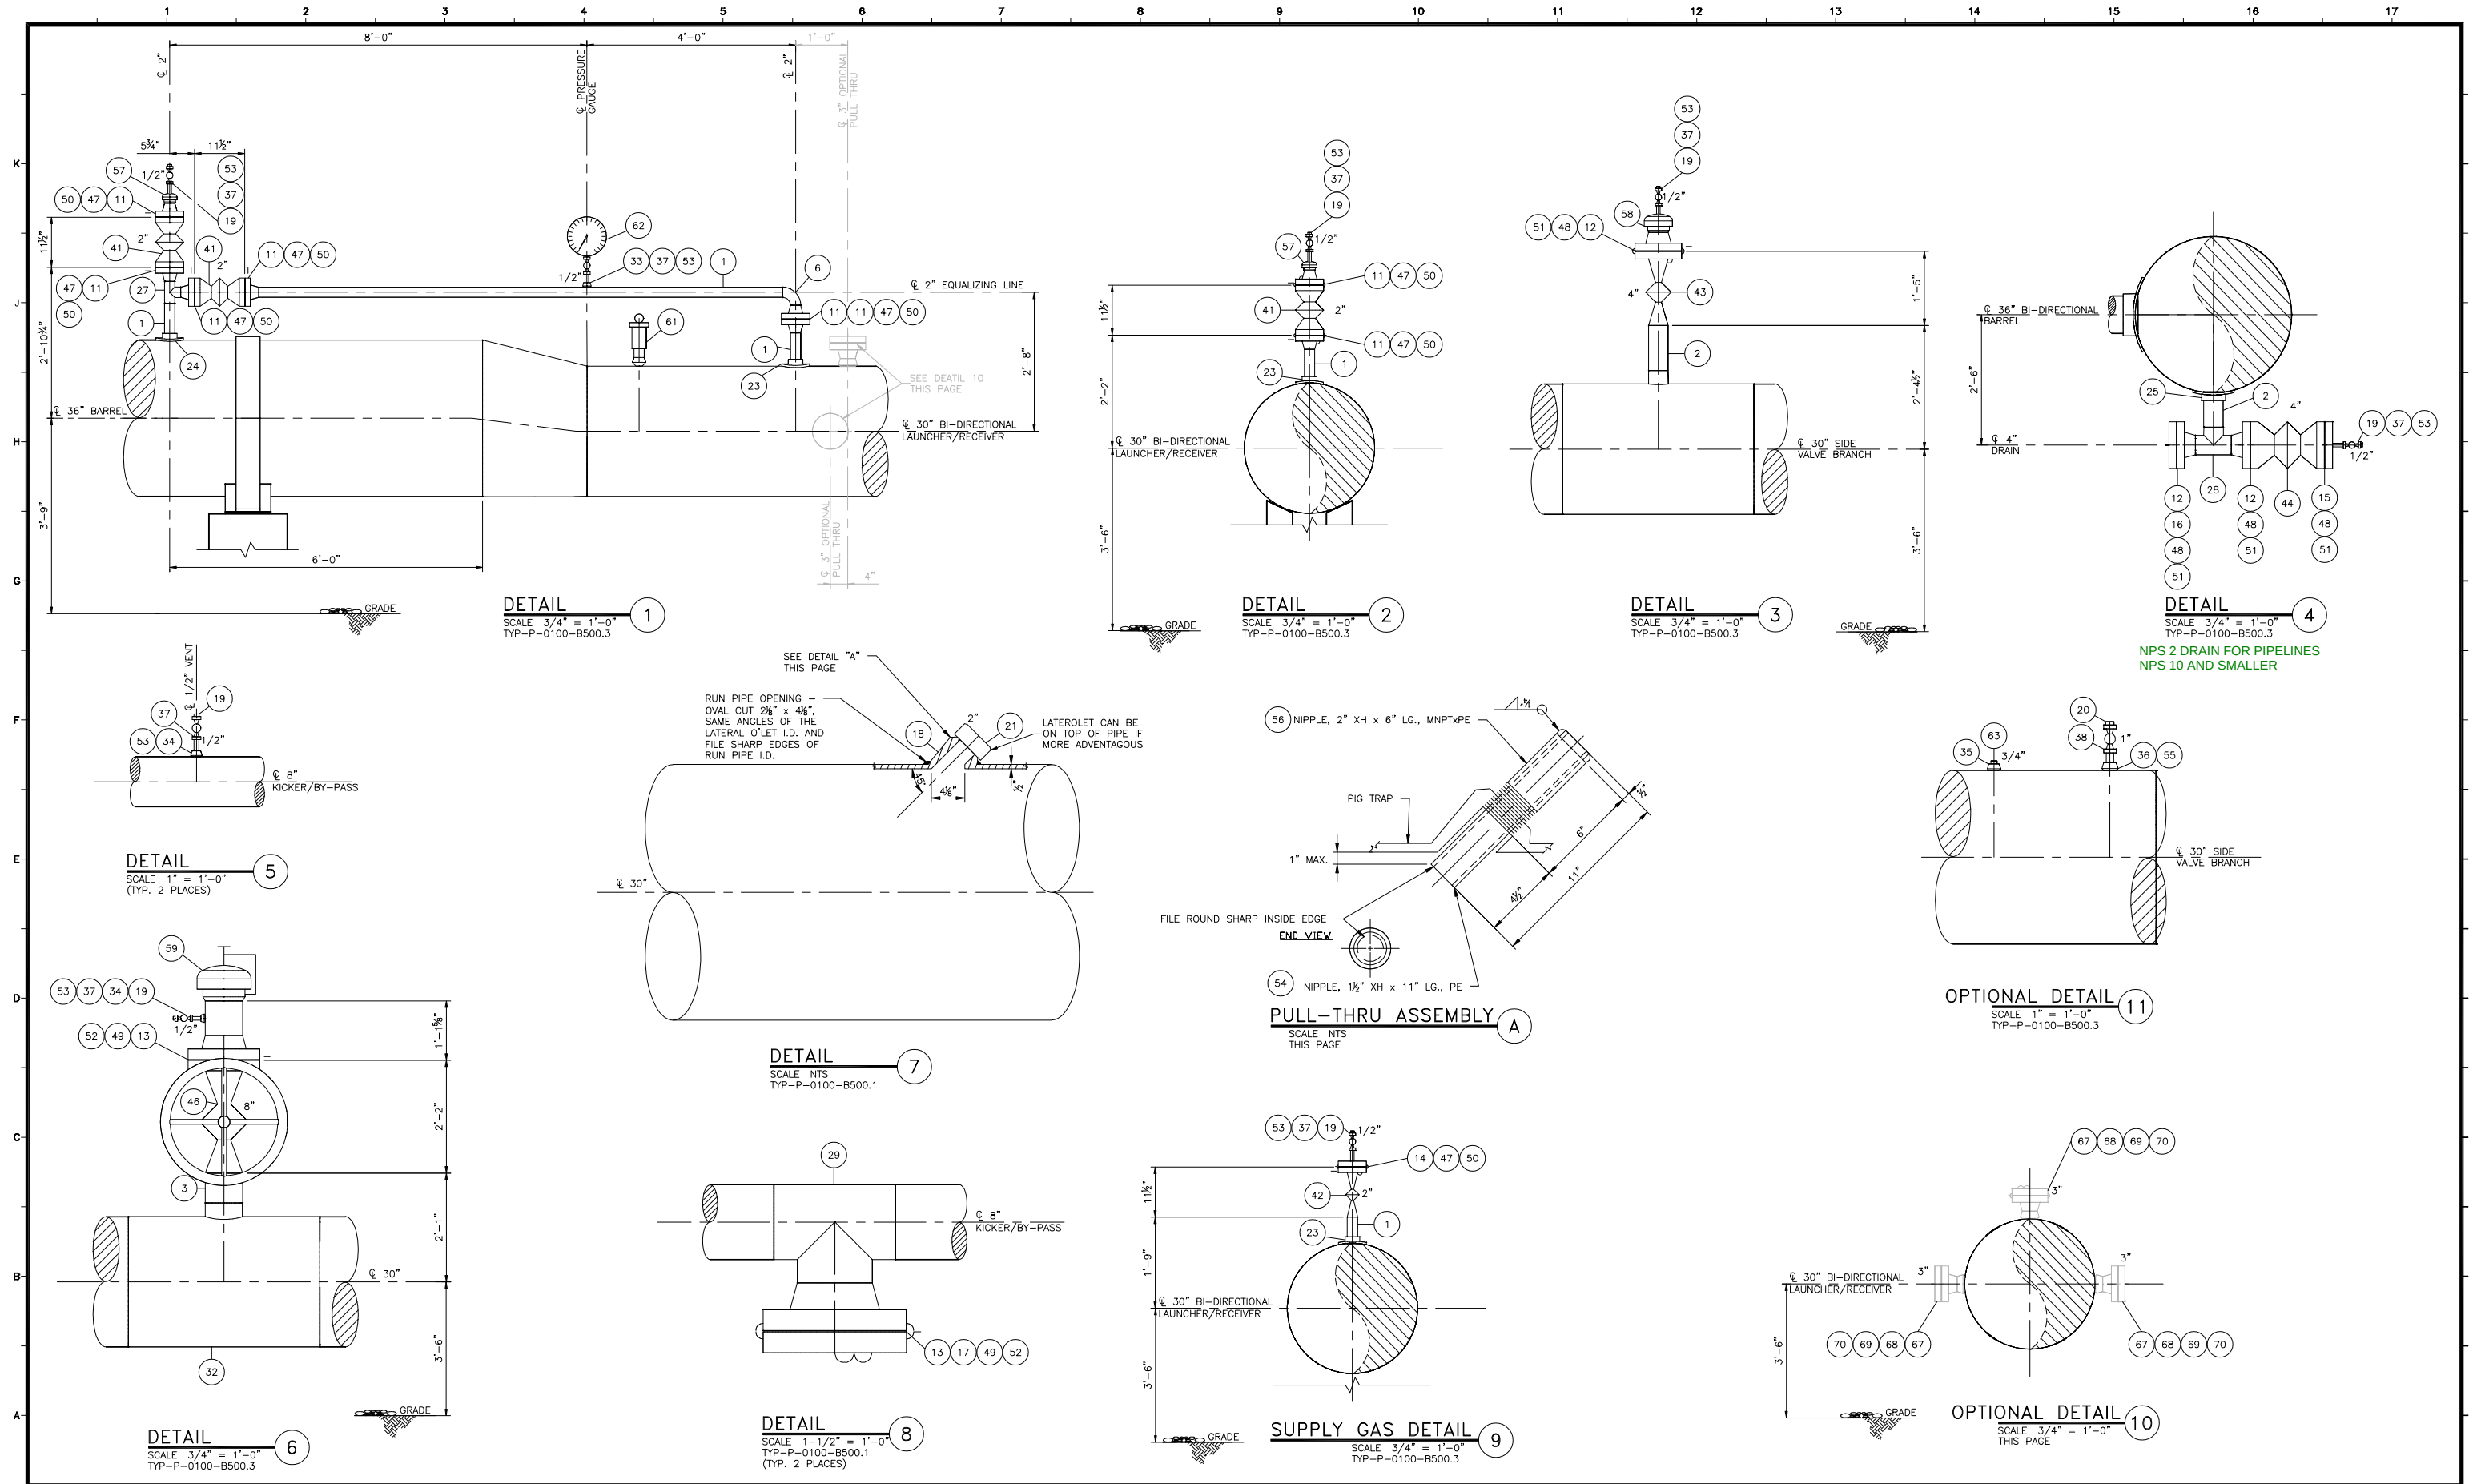

0	ISSUED FOR ADC APPROVAL	07-18-2022	
NO	Revision Description	Project ID	Date

NOTES:



Reference Drawings

PIPING DETAILS
30" BI-DIRECTIONAL LAUNCHER/RECEIVER

Status:	ISSUED FOR ADC APPROVAL
State:	PIN No:
County:	Scale: AS SHOWN
Category:	DETAIL
File Name:	TYP-P-0100-B500.4.dwg
Drawing No:	TYP-P-0100-B500.4
Rev	0

