




**SELECT WATER SOLUTIONS
CHK STATELINE PIPELINE
CIVIL & MECHANICAL DRAWING PACKAGE**

PANOLA COUNTY, TEXAS

CIVIL & MECHANICAL DRAWINGS			
REV.	DATE	DWG. NO.	DESCRIPTION
0	02/01/24	13932U000	COVER SHEET & DRAWING INDEX
0	02/01/24	13932L101	ARK WELL PAD RISER – PLAN, SECTIONS & BOM
0	02/01/24	13932L102	MAINLINE RISER 1 – PLOT PLAN
0	02/01/24	13932L103	MAINLINE RISER 1 – PLAN, SECTIONS & BOM
0	02/01/24	13932L104	SADDLER WELL PAD RISER – PLAN, SECTIONS & BOM
0	02/01/24	13932L105	CHK/NG RISER – PLOT PLAN
0	02/01/24	13932L106	CHK/NG RISER – PLAN, SECTIONS & BOM
0	02/01/24	13932L107	MAINLINE RISER 2 – PLOT PLAN
0	02/01/24	13932L108	MAINLINE RISER 2 – PLAN, SECTIONS & BOM
0	02/01/24	13932L109	METER RUN & CONTROL VALVE – PLOT PLAN
0	02/01/24	13932L110	METER RUN & CONTROL VALVE – PLAN
0	02/01/24	13932L111	METER RUN & CONTROL VALVE – SECTIONS
0	02/01/24	13932L112	METER RUN & CONTROL VALVE – BILL OF MATERIAL
0	02/01/24	13932M100	CONC. PEDESTAL PIPE SUPPORTS
0	02/01/24	13932M101	MAINLINE RISER 1 – PIPE FENCE DETAILS – PLAN, ELEVATION & BOM
0	02/01/24	13932M102	CHK/NG RISER – PIPE FENCE DETAILS – PLAN, ELEVATION & BOM
0	02/01/24	13932M103	MAINLINE RISER 2 – PIPE FENCE DETAILS – PLAN, ELEVATION & BOM
0	02/01/24	13932M104	METER RUN & CONTROL VALVE – PIPE FENCE DETAILS – PLAN, ELEVATION & BOM


**ISSUED FOR
CONSTRUCTION**
02/01/24



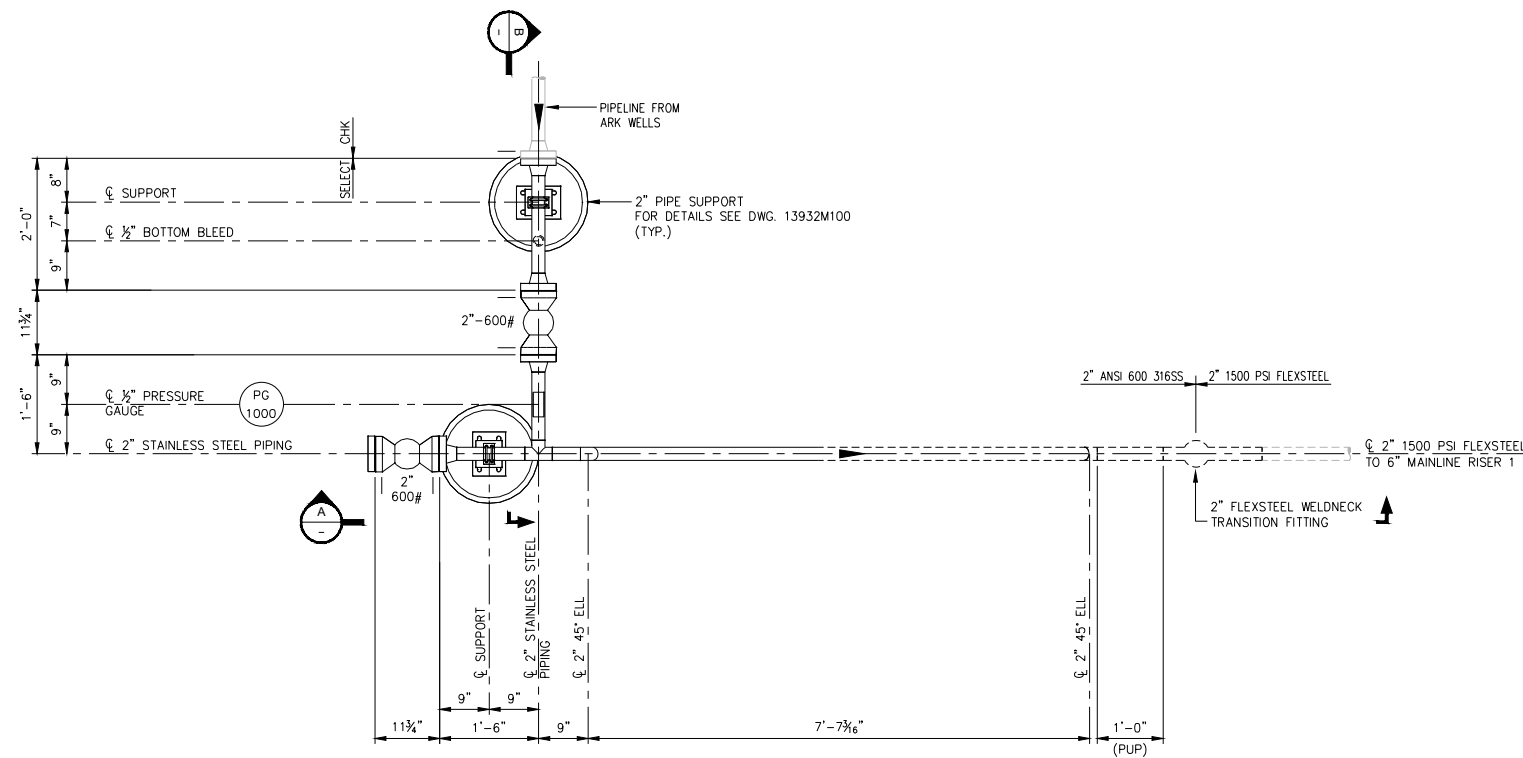

SECTION A-A


SCALE: 3/4"=1'-0"

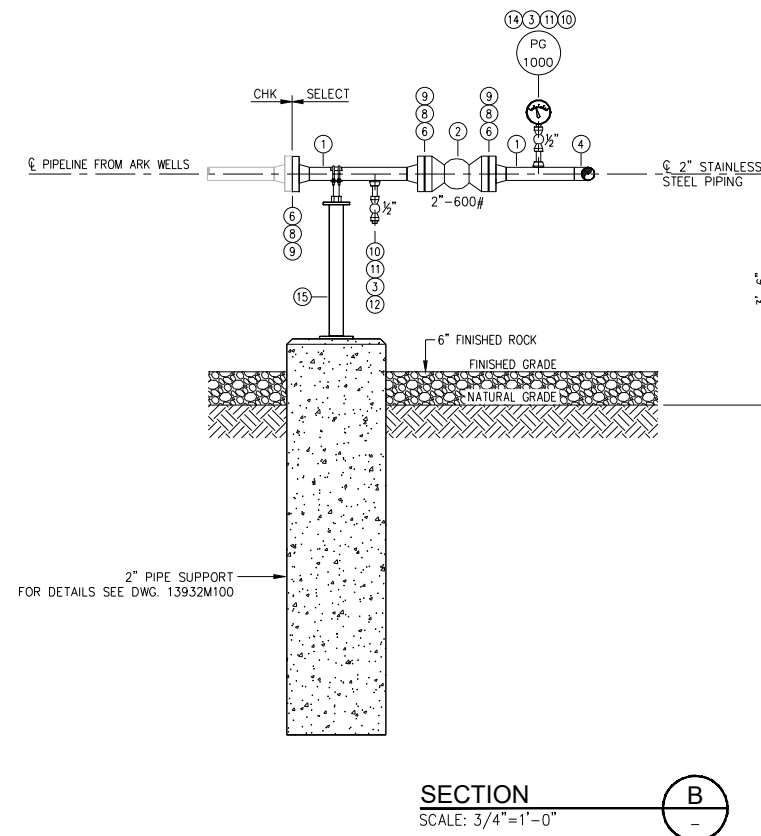

WBS NO.	
OLD DRAWING NO.	
—	
DRAWING NO.	REV. NO.
13932L101	0



WEST FORK
ENGINEERING

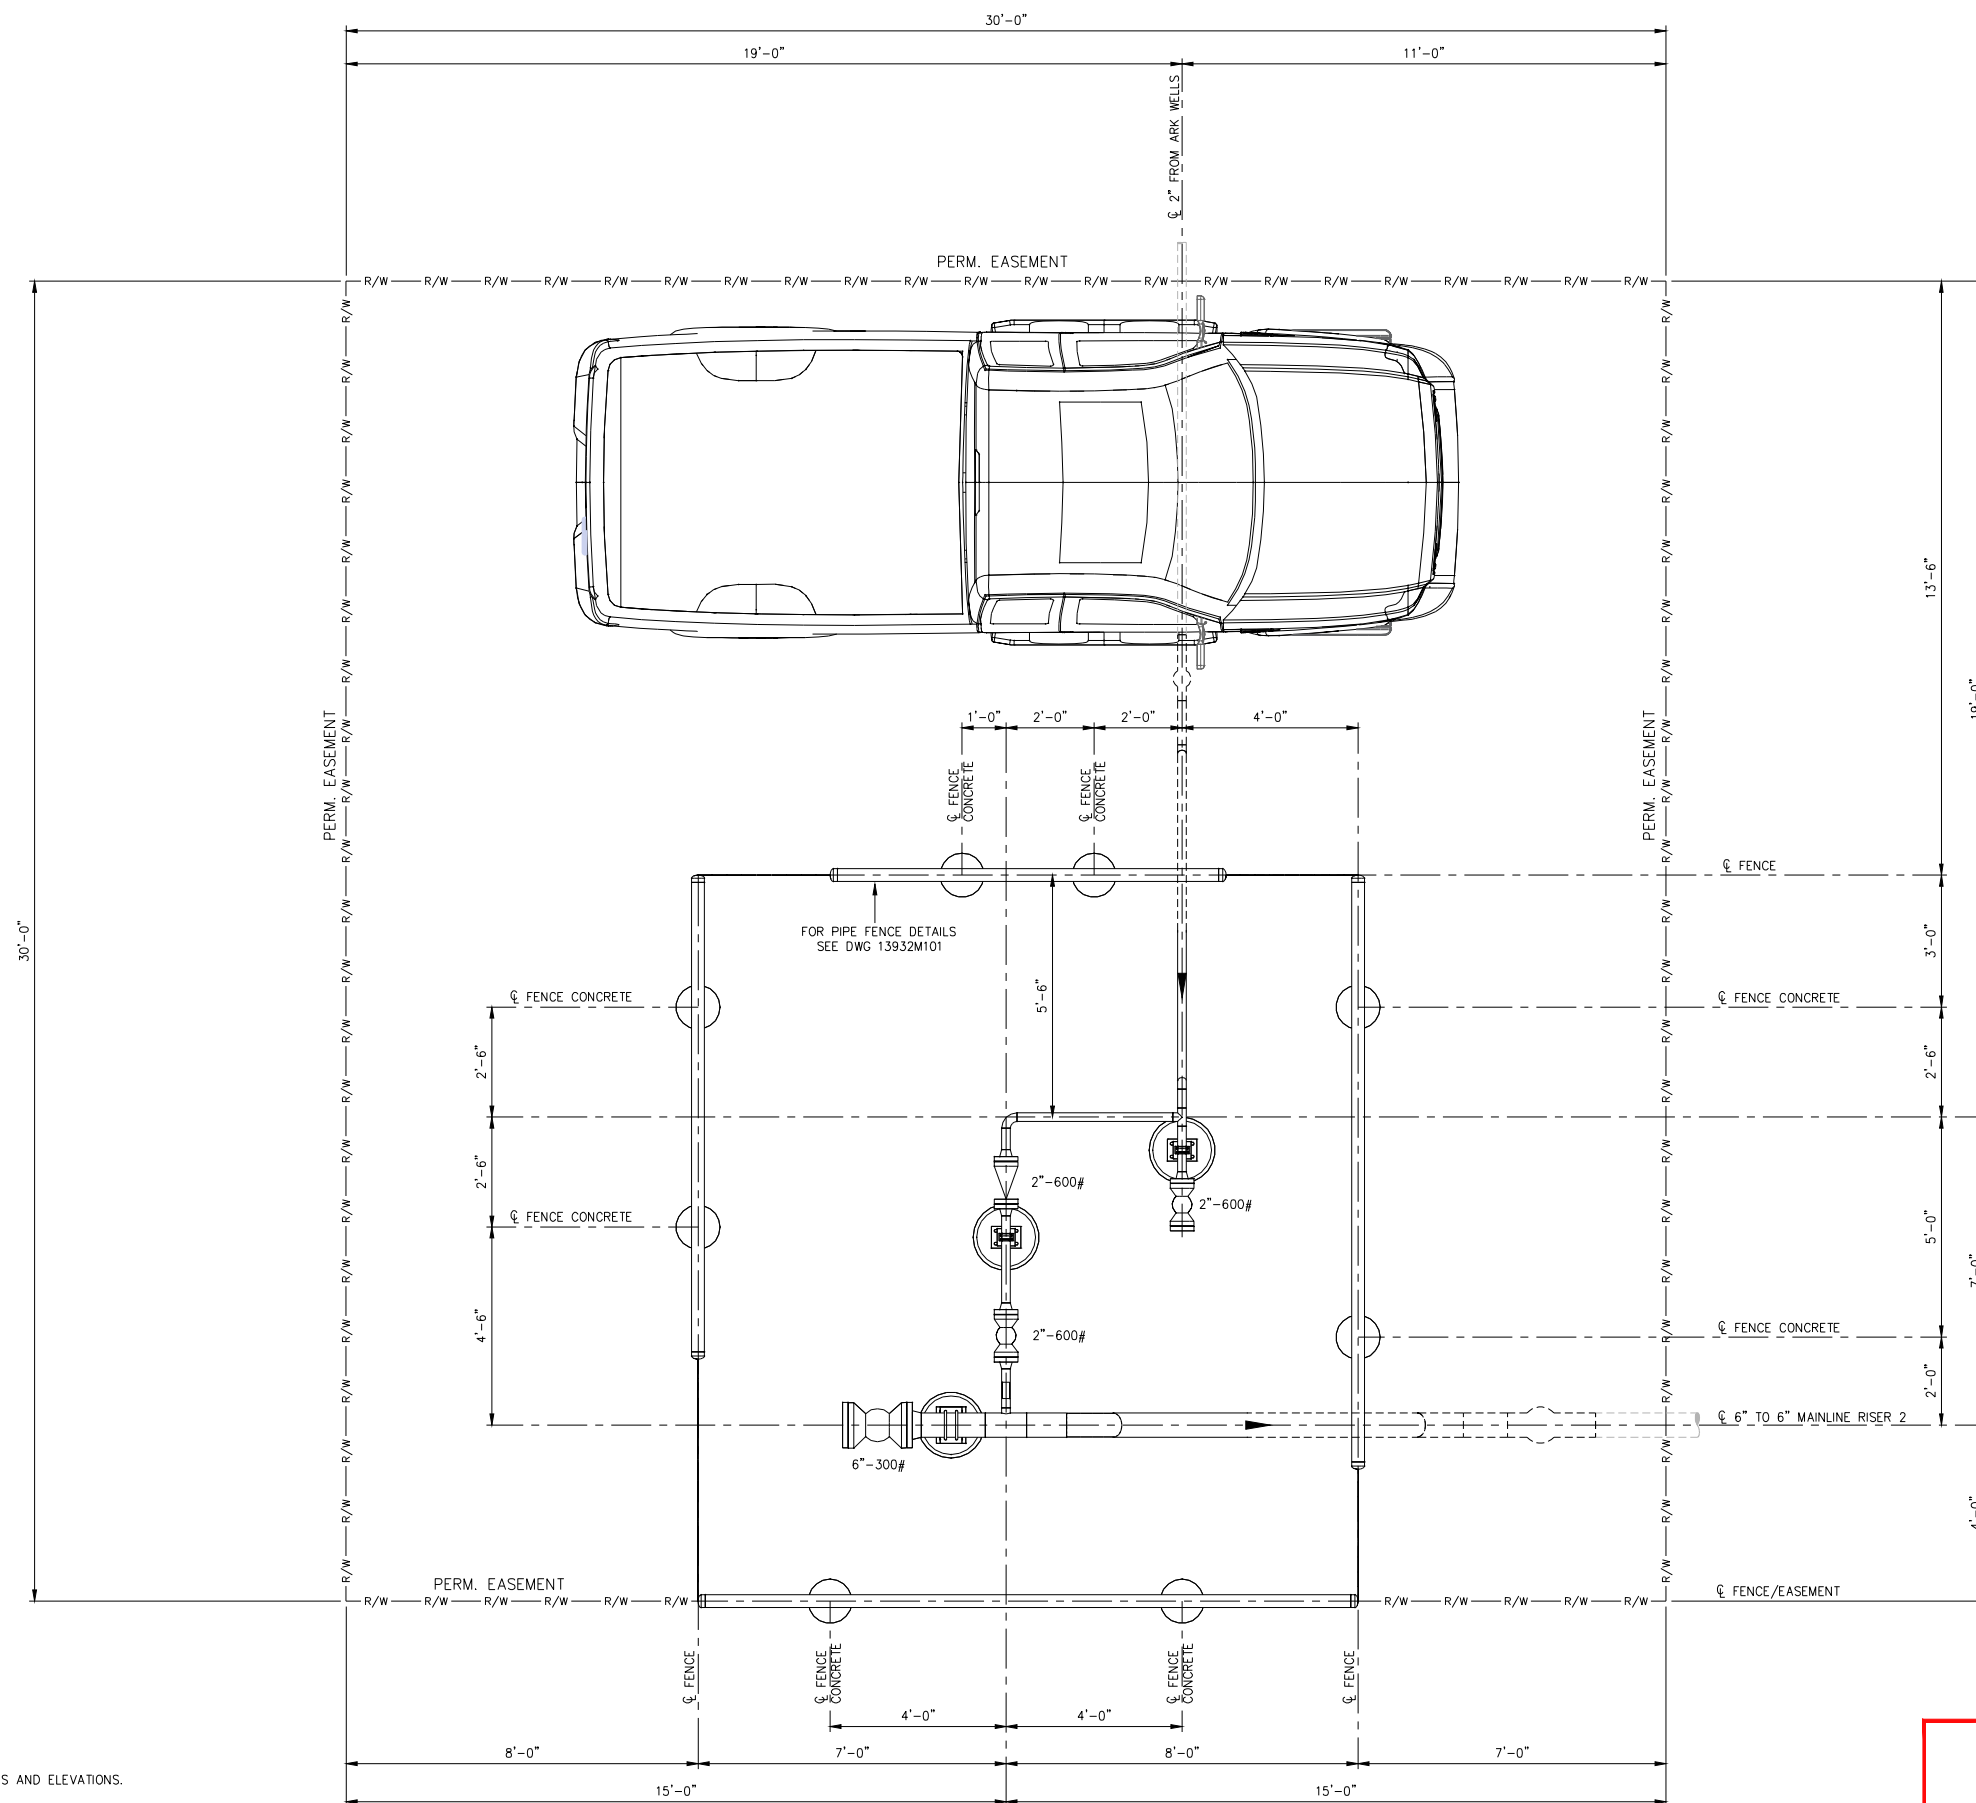

NOTE:

1. CONTRACTOR TO FIELD VERIFY ALL DIMENSIONS AND ELEVATIONS.
2. REFERENCE P&ID ON 13932-PID002
3. SEE PIPING DRAWING ON 13932L103 FOR DETAILS

**ISSUED FOR
CONSTRUCTION**
02/01/24



REFERENCE DRAWINGS								FACILITY CODE OR ACCOUNT NO:						CHK STATELINE PIPELINE MAINLINE RISER 1 PLOT PLAN				WBS NO.	
								CONSTRUCTION YEAR: 2024										OLD DRAWING NO.	
								DRAWN BY DATE										—	
								CHECK JM 01/11/24										DRAWING NO.	
O ISSUED FOR CONSTRUCTION				AT	02/01/24	ZR	JM	APPROVED JM 01/11/24						PANOLA COUNTY, TEXAS		13932L102		REV. NO.	
REV				DESCRIPTION				BY	DATE	CHK'D	APP'D	SCALE: 1/2"=1'-0"						0	



BILL OF MATERIAL – MAINLINE RISER 1				
MARK	SIZE	TOTAL QTY	DESCRIPTION	
1	2"	22'	PIPE–2.375" O.D. X 0.154" W.T.–SEAMLESS–ASTM A312–TP316/316L	
2	6"	15'	PIPE–6.625" O.D. X 0.280" W.T.–SEAMLESS–ASTM A312–TP316/316L BBE	
3	6"	1	VALVE, BALL, 6" ANSI 300, RFFE, FULL PORT, 316SS	
4	2"	2	VALVE, BALL, 2" ANSI 600, RFFE, FULL PORT, 316SS	
5	1/2"	2	BALL VALVE–THRD–CLASS 1500#, THRD X THRD, ASTM A–182 GR. F316, 316 SS BALL AND STEM, LEVER OPERATED, PTFE SEAT, FULL BORE, API 608 & API–607 (FIRE TESTED)	
6	2"	1	CHECK VALVE–SWING–ASME CLASS 600# RF– A–351 GR. CF3 BODY, 316 SS TRIM, BOLTED COVER, SS TRIM AND CLAPPER, SWING CHECK.	
7	2"	1	TEE, STRAIGHT, WELD, 2.375" O.D. 0.154" W.T., ASTM A403–WP316/316L–S–ASME B16.9	
8	6" x 2"	1	TEE, REDUCING, WELD, 6.625" O.D. 0.280" W.T. X 2.375" O.D., 0.154" W.T., ASTM A403–WP316/316L–S–ASME B16.9	
9	6"	2	ELL, WELD, 6.625" O.D. X 0.280" W.T., 45 DEGREE, 3R, STAINLESS STEEL, ASTM A403–WP316/316L–S–ASME B16.9	
10	2"	2	ELL, WELD, 2.375" O.D. X 0.154" W.T., 45 DEGREE, LR, STAINLESS STEEL, ASTM A403–WP316/316L–S–ASME B16.9	
11	6"	1	FLANGE, 6", ANSI 300, B.T.M. 0.280" W.T., RFWN, ASTM A182, F316/316L, ASME 16.5, GROUP 2.1	
12	2"	5	FLANGE, 2", ANSI 600, B.T.M. 0.154" W.T., RFWN, ASTM A182, F316/316L, ASME 16.5, GROUP 2.1	
13	6"	1	FLANGE, BLIND, 6", ANSI 300, RAISED FACE, ASTM A182, F316/316L, ASME 16.5.	
14	2"	1	FLANGE, BLIND, 2", ANSI 600, RAISED FACE, ASTM A182, F316/316L, ASME 16.5.	
15	6"	2	GASKET–ASME CLASS 300# RF–SPIRAL WOUND 1/8" THICK–316/316L SS OUTER RING–316 SS WINDING W/ FLEX GRAPHITE FILLER–316/316L SS INNER RING–ASME B16.20 FLEXITALLIC CGI	
16	2"	6	GASKET–ASME CLASS 600# RF–SPIRAL WOUND 1/8" THICK–316/316L SS OUTER RING–316/316L SS WINDING, FLEX GRAPHITE FILLER–316/316L SS INNER RING–ASME B16.20, FLEXITALLIC CGI	
17	6"	24	STUD BOLT SET, CS, 3/4" x 5" LONG, ASTM A–193, GR B7, w/2, ASTM A–194 CLASS 2H, HEX NUTS PER SET, TEFLON/XYLAN COATED (6" 300#; FLANGE, 12 PER SET)	
18	2"	48	STUD BOLT SET, CS, 5/8" x 4 1/2" LONG, ASTM A–193, GR B7, w/2, ASTM A–194 CLASS 2H, HEX NUTS PER SET, TEFLON/XYLAN COATED (2" 600#; FLANGE, 8 PER SET)	
19	1/2"	2	OUTLET, 1/2", THREADED, 2" THROUGH 36", 3000#, MSS SP–97 & ASTM A182 F316/316L	
20	1/2"	2	PIPE, NIPPLE, 1/2" x 3" LG, SCH 160, TBE, SMLS, B16.11 & ASTM A182 F316/316L	
21	6"	1	FLEXSTEEL WELDNECK TRANSITION FITTING	
22	2"	1	FLEXSTEEL WELDNECK TRANSITION FITTING	
23	1/2"	1	PRESSURE GAUGE, 0–1500 PSI, 4" DIAL, 1/2" MNPT, STEEL CASE U.S. GAUGE	
24	2"	2	SUPPORT, PIPE, EZ–LINE "F" TYPE, 2", W/ BASE PLATE AND 4 SLOTTED HOLES, 204–FIR, 2" P.S., D=2'–6".	
25	6"	1	SUPPORT, PIPE, EZ–LINE "F" TYPE, 6", W/ BASE PLATE AND 4 SLOTTED HOLES, 510–FIR, 6" P.S., D=2'–6".	
26	1/2"	1	PLUG, FORGED, HEX HEAD, THREADED, 1/2", 3000#, STAINLESS STEEL, B16.11 & ASTM A182 F316/316L, SOLID	
27	2"	1	ELL, WELD, 2.375" O.D. X 0.154" W.T., 90 DEGREE, LR, STAINLESS STEEL, ASTM A403–WP316/316L–S–ASME B16.9	



CHK STATELINE PIPELINE
CHK/NG RISER
PLOT PLAN

PANOLA COUNTY, TEXAS

NOTE:

1. CONTRACTOR TO FIELD VERIFY ALL DIMENSIONS AND ELEVATIONS.
2. REFERENCE P&ID ON 13932-PID004
3. SEE PIPING DRAWING ON 13932L106 FOR DETAILS

REFERENCE DRAWINGS	

0	ISSUED FOR CONSTRUCTION	AT	02/01/24	ZR	JM
REV	DESCRIPTION	BY	DATE	CHK'D	APP'D

FACILITY CODE OR ACCOUNT NO:		
CONSTRUCTION YEAR:		2024
	BY	DATE
DRAWN	AT	01/11/24
CHECK	JM	01/11/24
APPROVED	JM	01/11/24
SCALE: 1/2" = 1'-0"		



WBS NO.	
OLD DRAWING NO.	
—	
DRAWING NO.	REV. NO.
13932L105	0



DRAWING NO.	REV. NO.
13932L106	0

PANOLA COUNTY, TEXAS



FACILITY CODE		
OR ACCOUNT NO:		
CONSTRUCTION YEAR:		2024
	BY	DATE
DRAWN	AT	01/11/2
CHECK	JM	01/11/2
APPROVED	JM	01/11/2
SCALE: 1/2"=1'-0"		


0	ISSUED FOR CONSTRUCTION	AT	02/01/24	ZR	JM
REV.	DESCRIPTION	BY	DATE	CHECK'D	APP'D

REFERENCE DRAWINGS

1. CONTRACTOR TO FIELD VERIFY ALL DIMENSIONS AND ELEVATIONS.
2. REFERENCE P&ID 13932-PID004

FILENAME: D:\West Fork Engineering\CHK STATELINE PIPELINE\DRAWINGS\13932106.dwg PLOTTED: 1/31/2024 3:38:28 PM PLOTTED BY: ----

FILENAME: D:\West Fork Engineering\CHK STATELINE PIPELINE\DRAWINGS\13932L107.dwg PLOTTED: 1/31/2024 3:39:01 PM PLOTTED BY: -----

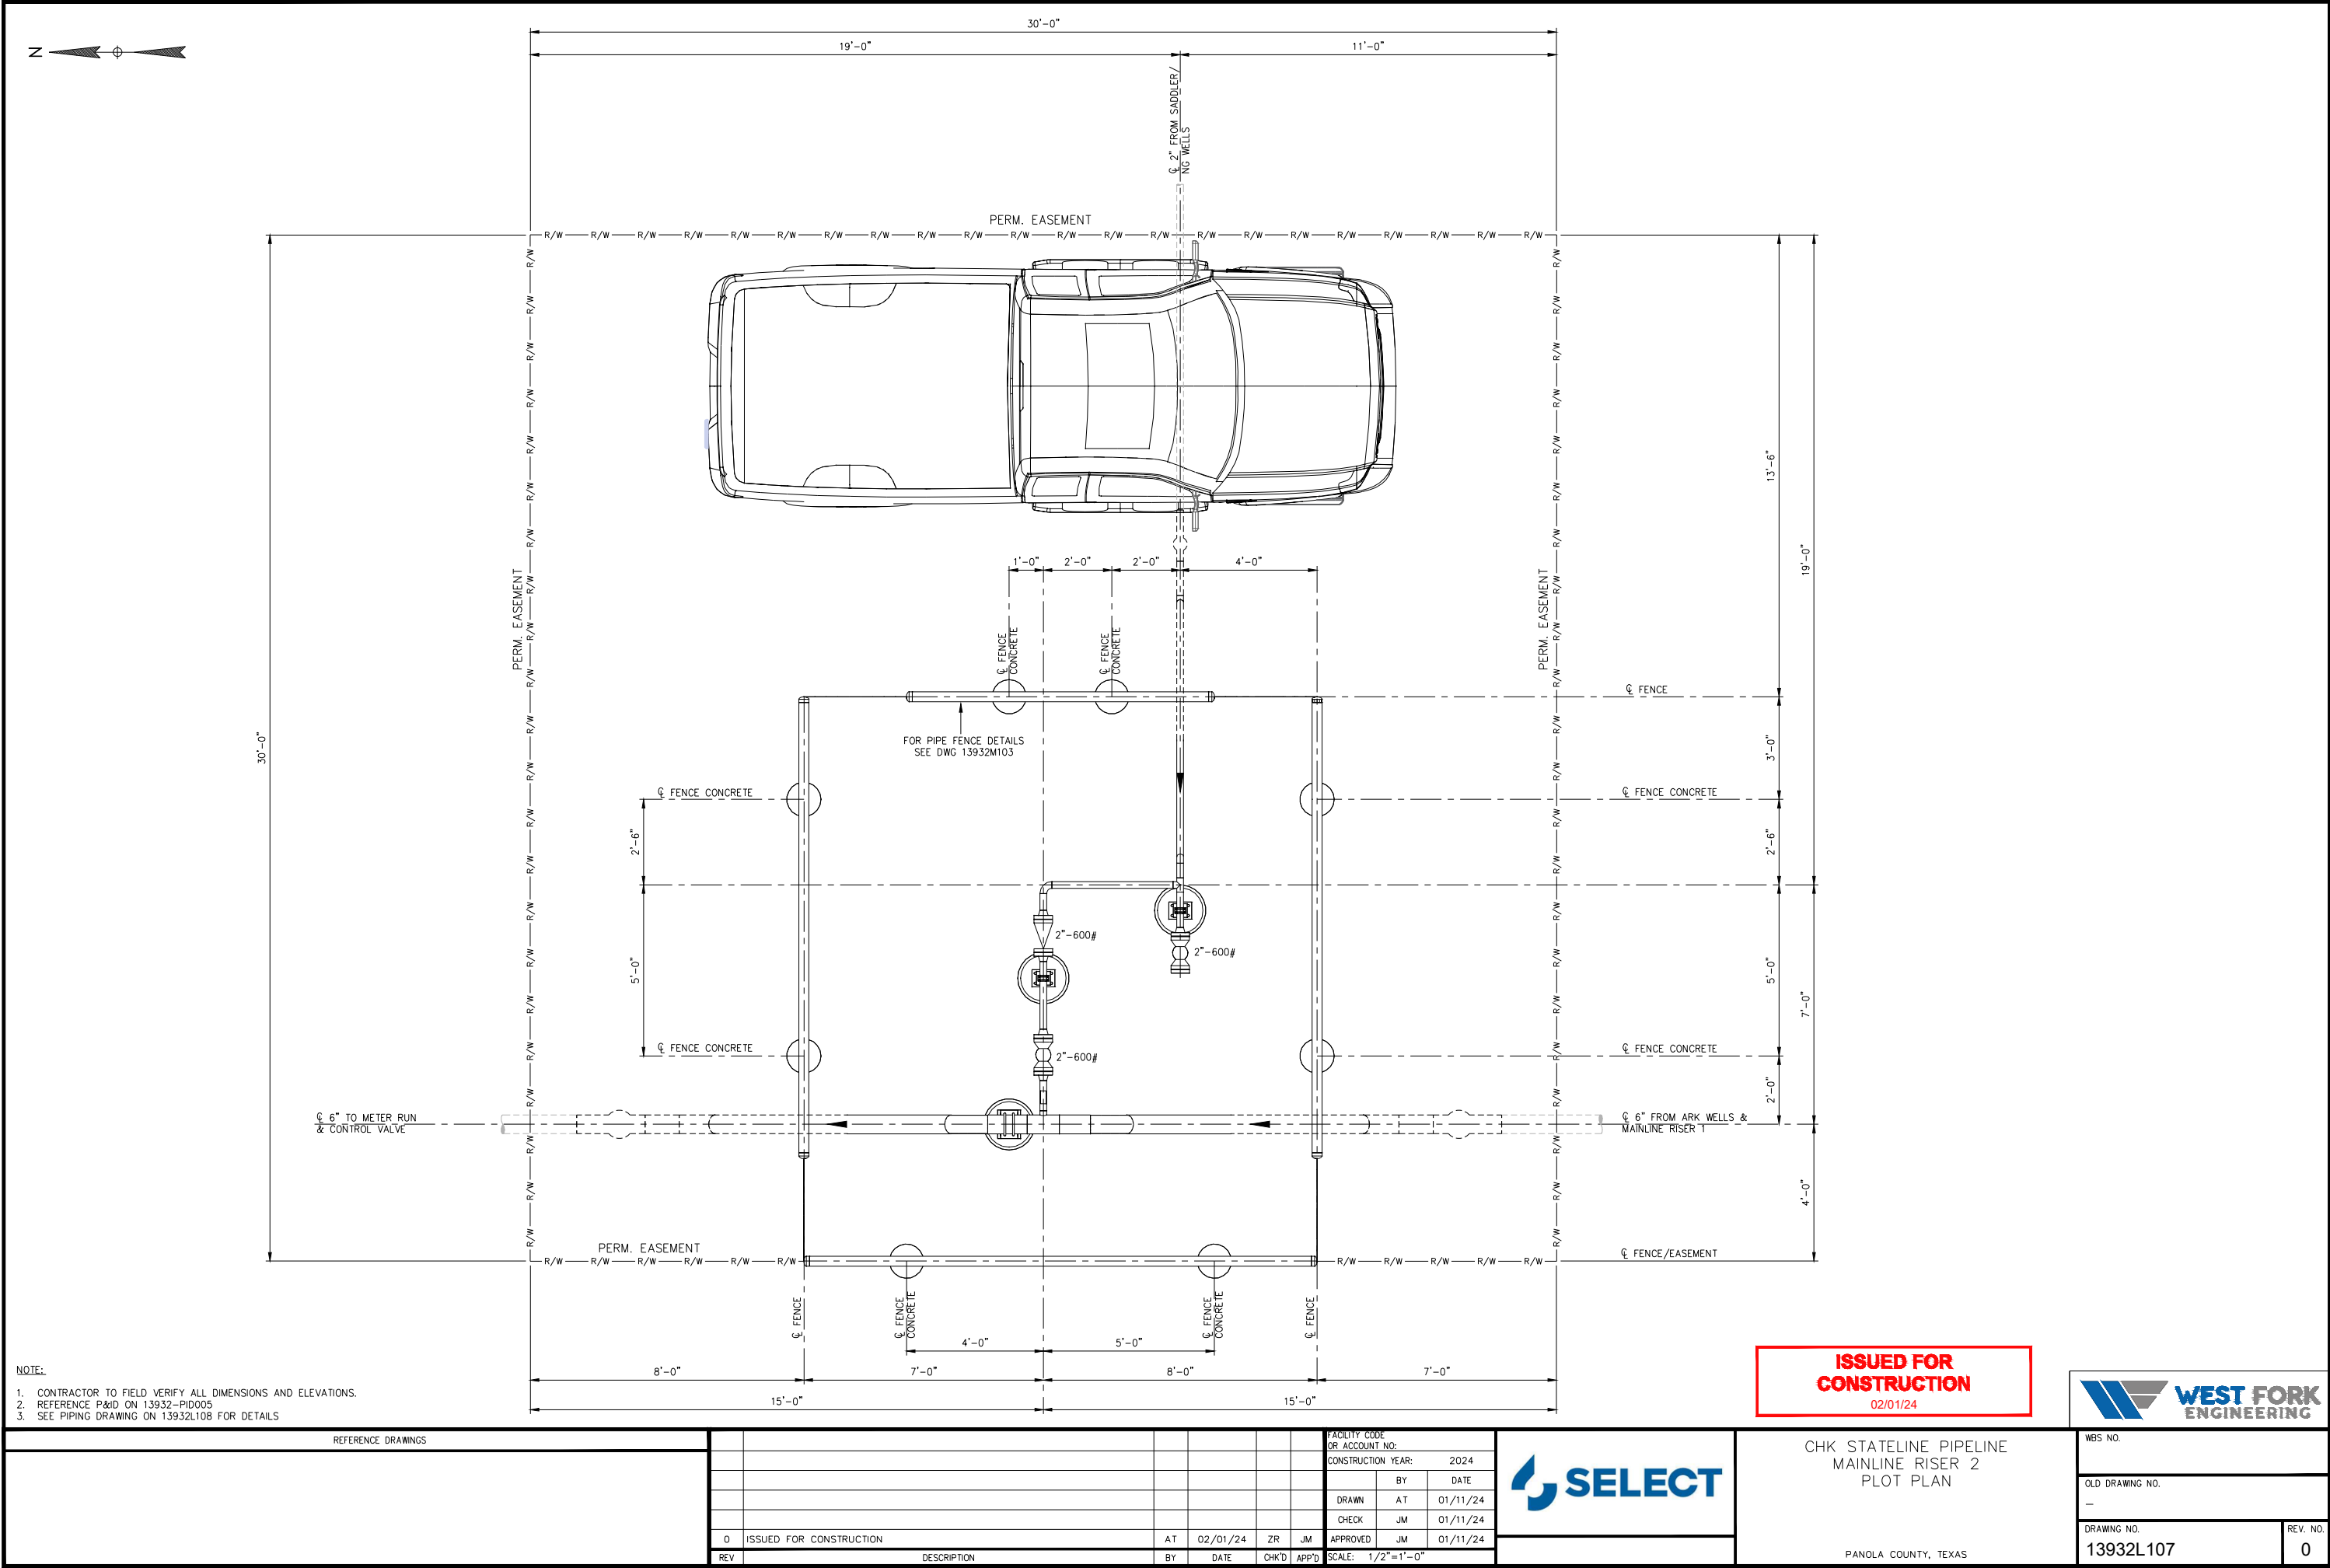

- NOTE:
1. CONTRACTOR TO FIELD VERIFY ALL DIMENSIONS AND ELEVATIONS.
 2. REFERENCE P&ID ON 13932-PID005
 3. SEE PIPING DRAWING ON 13932L108 FOR DETAILS

REFERENCE DRAWINGS				FACILITY CODE OR ACCOUNT NO:							CHK STATELINE PIPELINE MAINLINE RISER 2 PLOT PLAN		WBS NO.			
													OLD DRAWING NO.			
													DRAWING NO.			
													REV. NO.			
0				ISSUED FOR CONSTRUCTION				AT	02/01/24	ZR	JM	APPROVED	JM	01/11/24	13932L107	0
REV				DESCRIPTION				BY	DATE	CHK'D	APP'D	SCALE: 1/2"=1'-0"				

ISSUED FOR
CONSTRUCTION
02/01/24



PANOLA COUNTY, TEXAS



CHK STATELINE PIPELINE
MAINLINE RISER 2
PLAN, SECTIONS & BOM

PANOLA COUNTY, TEXAS

NOTE:

1. CONTRACTOR TO FIELD VERIFY ALL DIMENSIONS AND ELEVATIONS.
2. REFERENCE P&ID 13932-PID005


REFERENCE DRAWINGS	


0	ISSUED FOR CONSTRUCTION	AT	02/01/24	ZR	JM
REV	DESCRIPTION	BY	DATE	CHK'D	APP'D

FACILITY CODE		
OR ACCOUNT NO:		
CONSTRUCTION YEAR:		2024
	BY	DATE
DRAWN	AT	01/11/24
CHECK	JM	01/11/24
APPROVED	JM	01/11/24
SCALE: 1/2" = 1'-0"		



WBS NO.	
OLD DRAWING NO. —	
DRAWING NO. 13932L108	REV. NO. 0



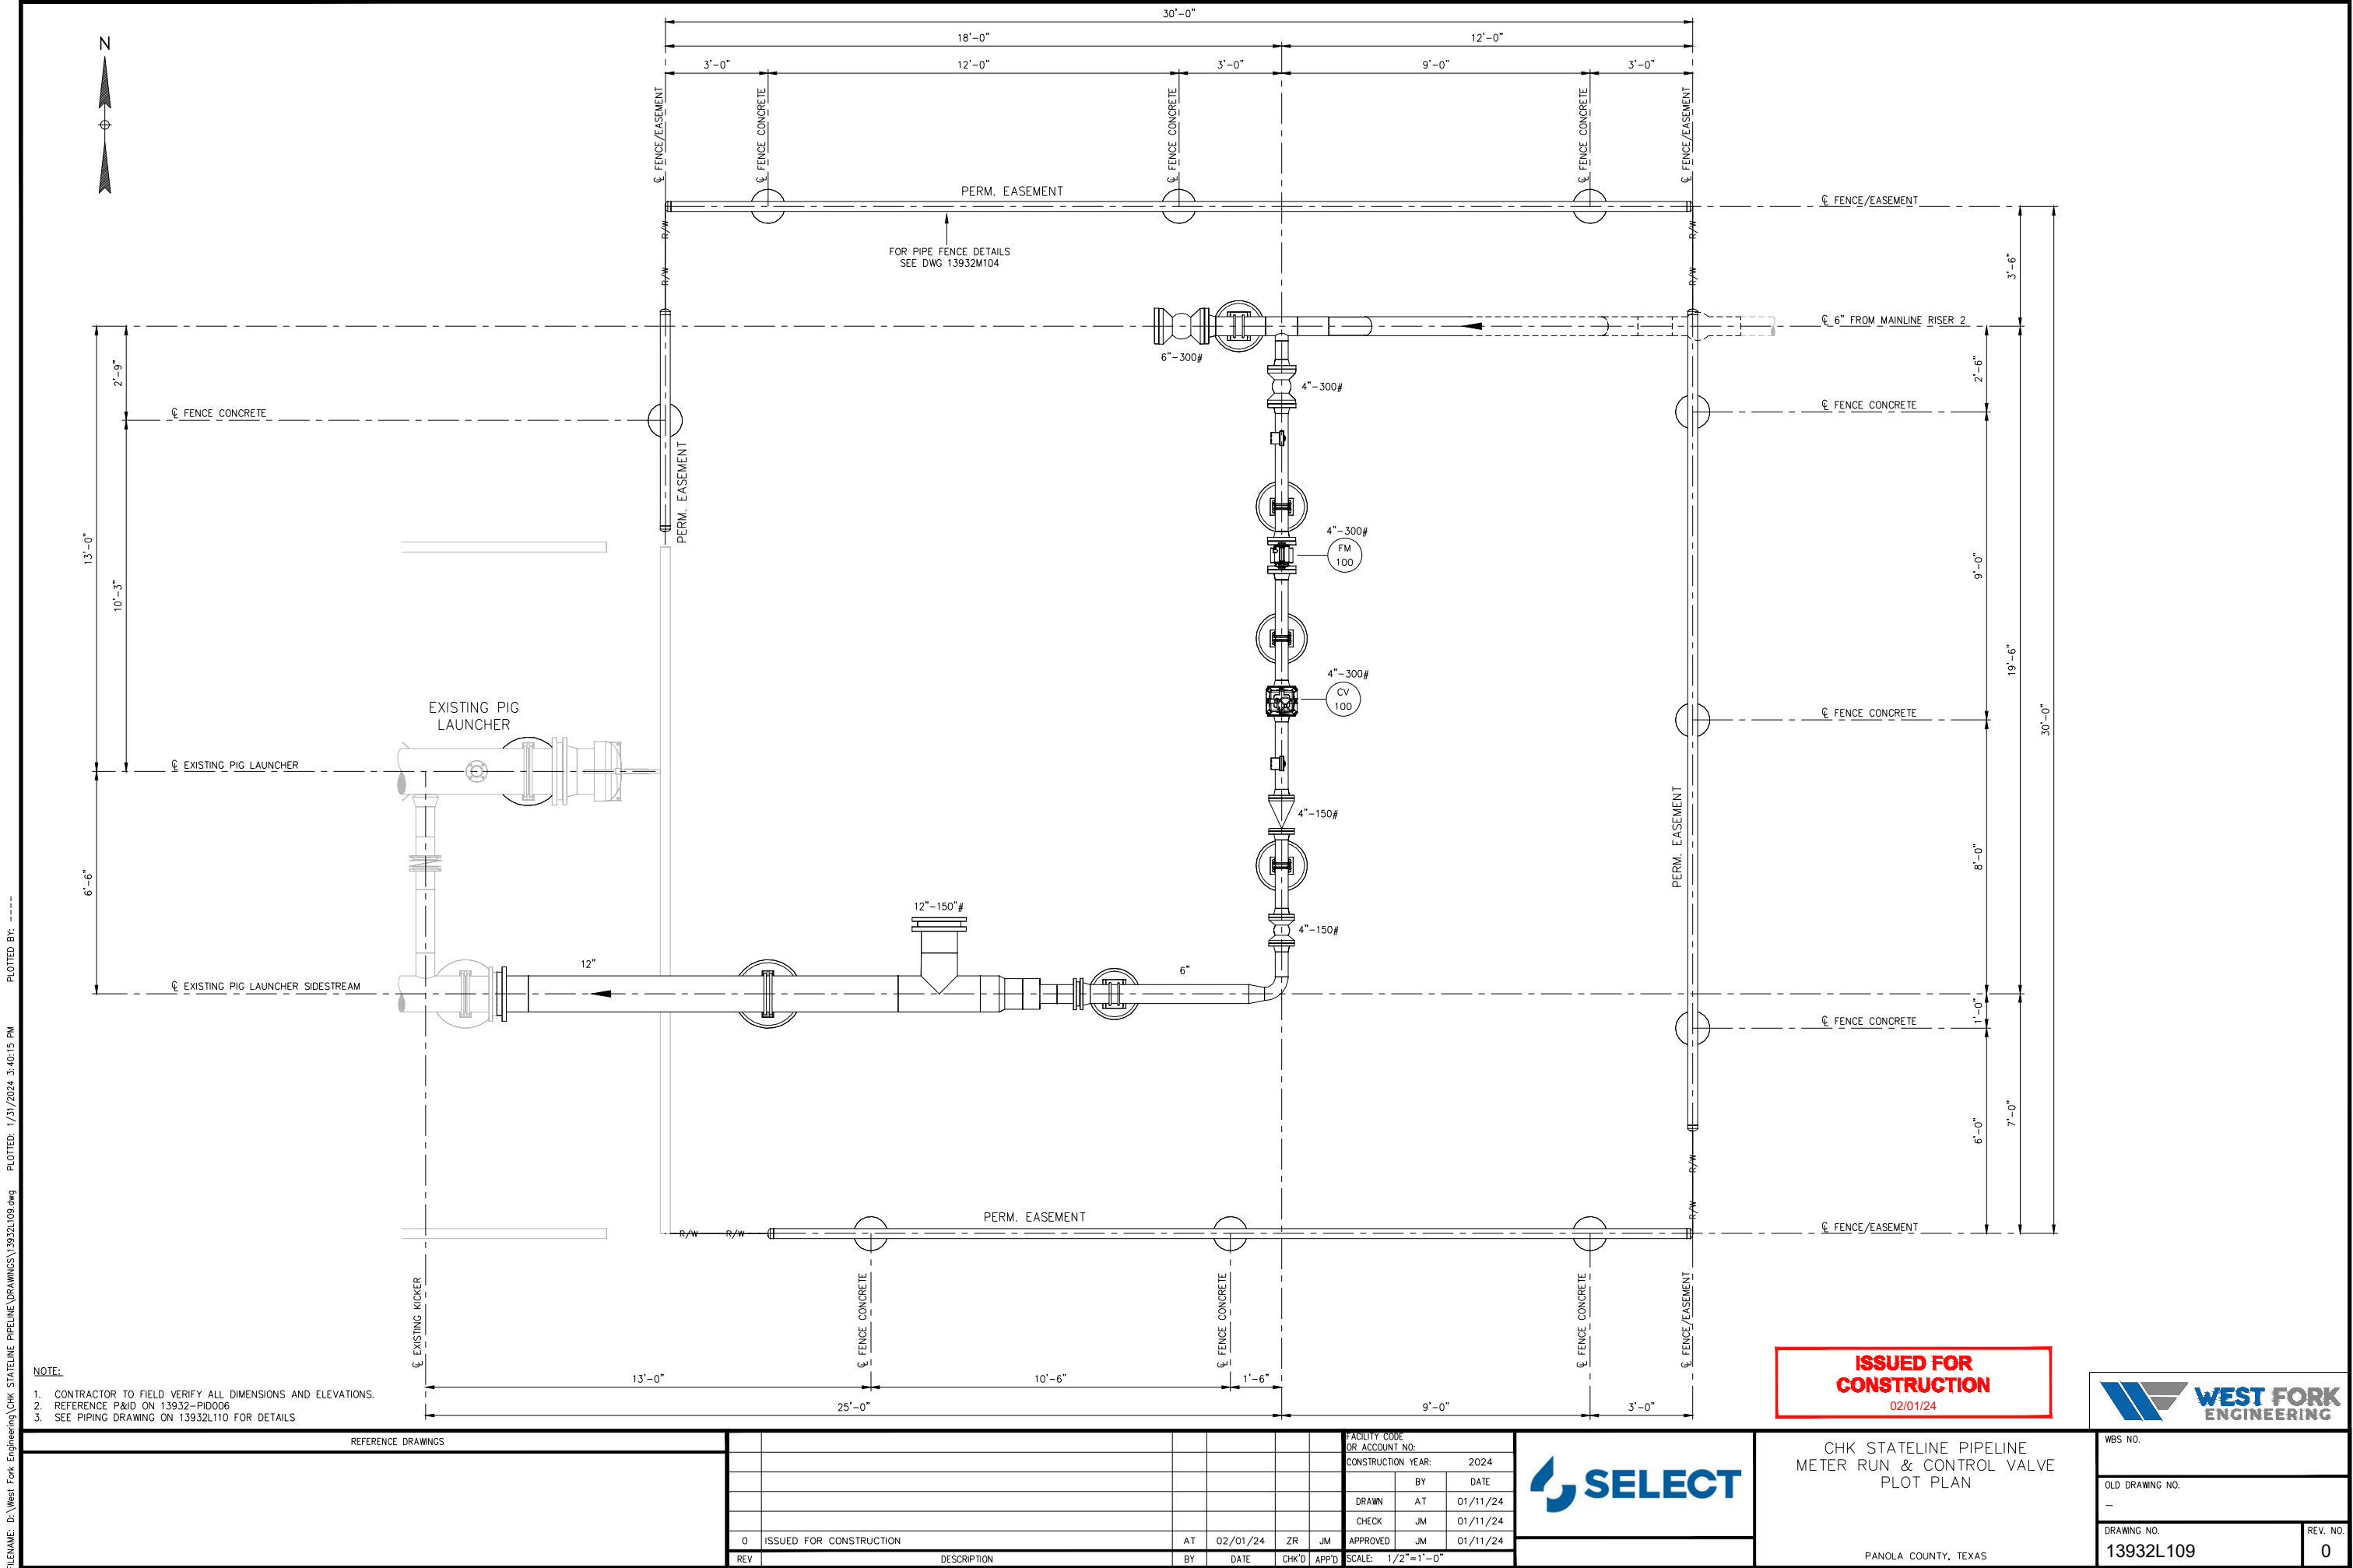


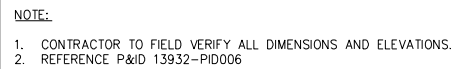

WEST FORK
ENGINEERING

REFERENCE DRAWINGS	
--------------------	--	--	

PANOLA COUNTY, TEXAS

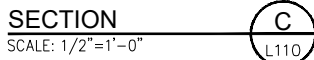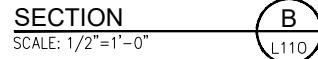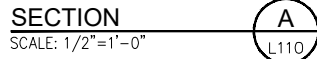

1. CONTRACTOR TO FIELD VERIFY ALL DIMENSIONS AND ELEVATIONS.
2. REFERENCE P&ID 13932-PID006

REFERENCE DRAWINGS																				FACILITY CODE OR ACCOUNT NO: CONSTRUCTION YEAR: 2024										 CHK STATELINE PIPELINE METER RUN & CONTROL VALVE SECTIONS PANOLA COUNTY, TEXAS										WBS NO.									
																				DRAWN AT 01/11/24																				OLD DRAWING NO. —									
																				CHECK JM 01/11/24																													
																				APPROVED JM 01/11/24																													
0 ISSUED FOR CONSTRUCTION										AT 02/01/24 ZR JM										SCALE: 3/8"=1'-0"																													
REV DESCRIPTION										BY DATE CHK'D APP'D																				DRAWING NO. 13932L111										REV. NO. 0									

**ISSUED FOR
CONSTRUCTION**
02/01/24



CHK STATELINE PIPELINE
METER RUN & CONTROL VALVE
SECTIONS

PANOLA COUNTY, TEXAS

WBS NO.	
OLD DRAWING NO.	
—	
DRAWING NO.	REV. NO.
13932L111	0

BILL OF MATERIAL — METER RUN & CONTROL VALVE			
MARK	SIZE	TOTAL QTY	DESCRIPTION
1	12"	15'	PIPE, 12" SDR 9, HDPE, IPS, PPI PE4710, ASTM D3350, CELL CLASS 445474C
2	4"	16'	PIPE—4.500" O.D. X 0.237" W.T.—SEAMLESS—ASTM A312—TP316/316L
3	6"	2	ELL, WELD, 6.625" O.D. X 0.280" W.T., 45 DEGREE, 3R, STAINLESS STEEL, ASTM A403-WP316/316L—S—ASME B16.9
4	6"	25'	PIPE—6.625" O.D. X 0.280" W.T.—SEAMLESS—ASTM A312—TP316/316L BBE
5	4"	1	ELL, WELD, 4.500" O.D. X 0.237" W.T., 90 DEGREE, LR, STAINLESS STEEL, ASTM A403-WP316/316L—S—ASME B16.9
6	12"	1	TEE, 12", FAB, HDPE, MFG STD SDR 9
7	4" x 2"	0	TEE, REDUCING, WELD, 4.500" O.D. 0.237" W.T. X 2.375" O.D., 0.154" W.T., ASTM A403—WP316/316L—S—ASME B16.9
8	6" x 4"	1	TEE, REDUCING, WELD, 6.625" O.D. 0.280" W.T. X 4.500" O.D., 0.237" W.T., ASTM A403—WP316/316L—S—ASME B16.9 (WITH PIG BARS)
9	10" x 6"	1	REDUCER, 10"x6", CONC, HDPE, MFG STD SDR 9
10	12" x 10"	1	REDUCER, 12"x10" CONC, HDPE, MFG STD SDR 9
11	6" x 4"	1	REDUCER, CONC., WELD, 6.625" O.D. 0.280" W.T. X 4.500" O.D., 0.237" W.T., ASTM A403—WP316/316L—S—ASME B16.9
12	2"	0	FLANGE, 2", ANSI 600, B.T.M. 0.154" W.T., RFWN, ASTM A182, F316/316L, ASME 16.5, GROUP 2.1
13	4"	4	FLANGE, 4", ANSI 150, B.T.M. 0.237" W.T., RFWN, ASTM A182, F316/316L, ASME 16.5, GROUP 2.1
14	4"	6	FLANGE, 4", ANSI 300, B.T.M. 0.237" W.T., RFWN, ASTM A182, F316/316L, ASME 16.5, GROUP 2.1
15	6"	1	FLANGE, 6", ANSI 150, B.T.M. 0.280" W.T., RFWN, ASTM A182, F316/316L, ASME 16.5, GROUP 2.1
16	6"	1	FLANGE, 6", ANSI 300, B.T.M. 0.280" W.T., RFWN, ASTM A182, F316/316L, ASME 16.5, GROUP 2.1
17	12"	1	FLANGE, BLIND, 12", ANSI 150, RAISED FACE, ASTM A182, F316/316L, ASME 16.5.
18	2"	0	FLANGE, BLIND, 2", ANSI 600, RAISED FACE, ASTM A182, F316/316L, ASME 16.5.
19	6"	1	FLANGE, BLIND, 6", ANSI 300, RAISED FACE, ASTM A182, F316/316L, ASME 16.5.
20	12"	2	FLANGE ADAPTER BACKUP RING, 12", HDPE, IPS, , PPI PE4710, ASTM D3350
21	6"	1	FLANGE ADAPTER BACKUP RING, 6", HDPE, IPS, , PPI PE4710, ASTM D3350
22	6"	24	STUD BOLT SET, CS, 3/4" x 5" LONG, ASTM A—193, GR B7, w/2, ASTM A—194 CLASS 2H, HEX NUTS PER SET, TEFLON/XYLAN COATED (6' 300#; FLANGE, 12 PER SET)
23	4"	48	STUD BOLT SET, CS, 3/4" x 4 3/4" LONG, ASTM A—193, GR B7, w/2, ASTM A—194 CLASS 2H, HEX NUTS PER SET, TEFLON/XYLAN COATED (4' 300#; FLANGE,8 PER SET)
24	6"	8	STUD BOLT SET, CS, 3/4" x 5 1/2" LONG, ASTM A—193, GR B7, w/2, ASTM A—194 CLASS 2H, HEX NUTS PER SET, TEFLON/XYLAN COATED (6" 150#; FLANGE ADAPTER TO RF,8 PER SET)
25	4"	32	STUD BOLT SET, CS, 5/8" x 3 3/4" LONG, ASTM A—193, GR B7, w/2, ASTM A—194 CLASS 2H, HEX NUTS PER SET, TEFLON/XYLAN COATED (4' 150#; FLANGE,8 PER SET)
26	12"	12	STUD BOLT SET, CS, 7/8" x 10" LONG, ASTM A—193, GR B7, w/2, ASTM A—194 CLASS 2H, HEX NUTS PER SET, TEFLON/XYLAN COATED (12" 150#; FLANGE ADAPTER TO FLANGE ADAPTER ,12 PER SET)
27	12"	12	STUD BOLT SET, CS, 7/8" x 7 1/2" LONG, ASTM A—193, GR B7, w/2, ASTM A—194 CLASS 2H, HEX NUTS PER SET, TEFLON/XYLAN COATED (12" 150#; FLANGE ADAPTER TO RF,12 PER SET)




28	12"	0	GASKET-ASME CLASS 150# RF-SPIRAL WOUND 1/8" THICK-316/316L SS OUTER RING-316/316L SS WINDING, FLEX GRAPHITE FILLER-316/316L SS INNER RING-ASME B16.20, FLEXITALLIC CGI
29	12"	1	GASKET, GARLOCK, 12", ANSI 150, GYLON 3760 (STANDARD RINGS)
30	2"	0	GASKET-ASME CLASS 600# RF-SPIRAL WOUND 1/8" THICK-316/316L SS OUTER RING-316/316L SS WINDING, FLEX GRAPHITE FILLER-316/316L SS INNER RING-ASME B16.20, FLEXITALLIC CGI
31	4"	4	GASKET-ASME CLASS 150# RF-SPIRAL WOUND 1/8" THICK-316/316L SS OUTER RING-316/316L SS WINDING, FLEX GRAPHITE FILLER-316/316L SS INNER RING-ASME B16.20, FLEXITALLIC CGI
32	4"	6	GASKET-ASME CLASS 300# RF-SPIRAL WOUND 1/8" THICK-316/316L SS OUTER RING-316/316L SS WINDING, FLEX GRAPHITE FILLER-316/316L SS INNER RING-ASME B16.20, FLEXITALLIC CGI
33	6"	2	GASKET-ASME CLASS 300# RF-SPIRAL WOUND 1/8" THICK-316/316L SS OUTER RING-316/316L SS WINDING, FLEX GRAPHITE FILLER-316/316L SS INNER RING-ASME B16.20, FLEXITALLIC CGI
34	6"	1	GASKET, GARLOCK, 6", ANSI 150, GYLON 3760 (STANDARD RINGS)
35	1"	4	PIPE, NIPPLE, 1" x 3" LG, SCH 160, TBE, SMLS, B16.11 & ASTM A182 F316/316L
36	1"	2	PLUG, FORGED, HEX HEAD, THREADED, 1", 3000#, STAINLESS STEEL, B16.11 & ASTM A182 F316/316L, SOLID
37	1"	4	OUTLET, 1", THREADED, 2" THROUGH 36", 3000#, MSS SP-97 & ASTM A182 F316/316L
38	1"	4	BALL VALVE-THRD-CLASS 1500#, THRD x THRD, ASTM A-182 GR. F316, 316 SS BALL AND STEM, LEVER OPERATED, PTFE SEAT, FULL BORE, API 608 & API-607 (FIRE TESTED)
39	12"	1	SUPPORT, PIPE, EZ-LINE "F" TYPE, 12", W/ BASE PLATE AND 4 SLOTTED HOLES, 1218-FIR, 6" P.S., D=2'-6"
40	4"	1	VALVE, BALL, 4" ANSI 300, RFFE, FULL PORT, 316SS
41	4"	1	VALVE, BALL, 4" ANSI 300, RFFE, FULL PORT, 316SS
42	6"	1	VALVE, BALL, 6" ANSI 300, RFFE, FULL PORT, 316SS
43	4"	1	CHECK VALVE-SWING-ASME CLASS 150# RF- A-351 GR. CF3 BODY, 316 SS TRIM, BOLTED COVER, SS TRIM AND CLAPPER, SWING CHECK
44	4"	1	CONTROL VALVE- 300# RF, SEG V-BALL, SS316, J-FLOW, W/ SUPERCAPACITOR
45	12"	2	FLANGE ADAPTER, BEVELED, HDPE, IPS, MFG STD SDR 9, PPI PE4710, ASTM D3350, CELL CLASS 445474C
46	6"	1	FLANGE ADAPTER, BEVELED, HDPE, IPS, MFG STD SDR 9, PPI PE4710, ASTM D3350, CELL CLASS 445474C
47	4"	1	4" MAG METER, ANSI 300, SS316, MODUS, 24DC
48	6"	1	FLEXSTEEL WELDNECK TRANSITION FITTING
49	6"	2	SUPPORT, PIPE, EZ-LINE "F" TYPE, 6", W/ BASE PLATE AND 4 SLOTTED HOLES, 510-FIR, 6" P.S., D=2'-6"
50	4"	3	SUPPORT, PIPE, EZ-LINE "F" TYPE, 4", W/ BASE PLATE AND 4 SLOTTED HOLES, 204-FIR, 4" P.S., D=2'-6"
51	2"	2	PRESSURE TRANSMITTER, YOKOGAWA DPHARP DIGITAL DIRECT MOUNT GAUGE PRESSURE TRANSMITTER, 2 WIRE, 24 VDC, MWP POWERED, STANDARD CE MARK, SIL II CERTIFIED, 4-20 MADC OUTPUT W/ HART 5/7 PROTOCOL, 0-720 to 0-7200 PSI MIN/MAX SPAN, HASTELLOY C DIAPHRAGM/316SS FLANGES, 0.5" MNPT PROCESS CONNECTION, CAST-ALUMINUM ALLOY AMP HOUSING, 1/2" FNPT ELECTRICAL CONN. /2 PORTS, W/LCD DIGITAL INDICATOR W/ RANGE SWITCH, 316SS 2" PIPE MOUNT BRACKET, COMBINED /FF1 AND /FS1. UNIT OF MWP ON DP EXPRESSED IN PSI.

**ISSUED FOR
CONSTRUCTION**
02/01/24




REFERENCE DRAWINGS								FACILITY CODE OR ACCOUNT NO:				CHK STATELINE PIPELINE METER RUN & CONTROL VALVE BILL OF MATERIAL		WBS NO.	
								CONSTRUCTION YEAR: 2024						OLD DRAWING NO. —	
								BY DATE DRAWN AT 01/11/24 CHECK JM 01/11/24							
								APPROVED JM 01/11/24							
0 ISSUED FOR CONSTRUCTION				AT	02/01/24	ZR	JM	SCALE: 1/2"=1'-0"						DRAWING NO.	
REV	DESCRIPTION			BY	DATE	CHK'D	APP'D				13932L112		0		
											PANOLA COUNTY, TEXAS				

FILENAME: D:\West Fork Engineering\CHK STATELINE PIPELINE\DRAWINGS\13932M100.dwg PLOTTED: 1/31/2024 3:48:28 PM PLOTTED BY: -----

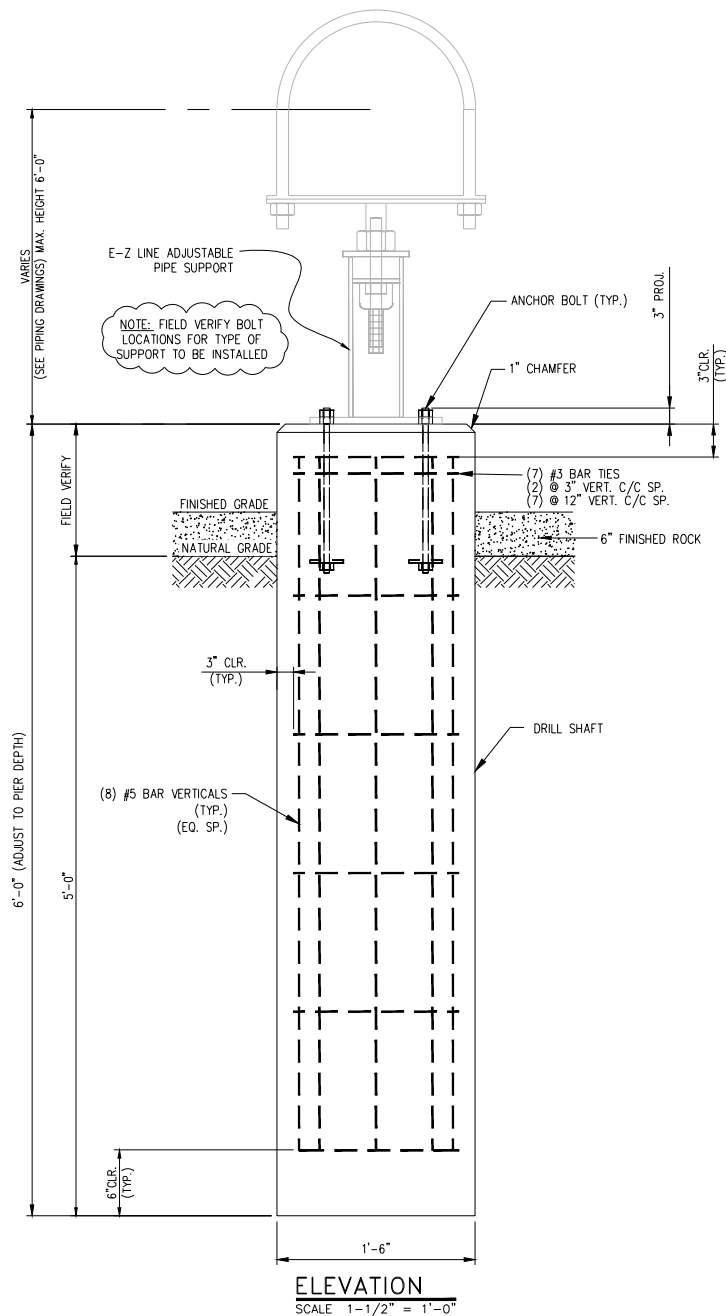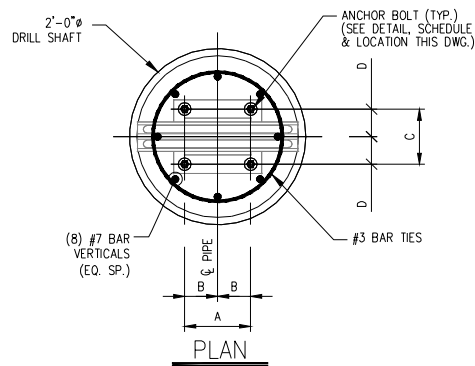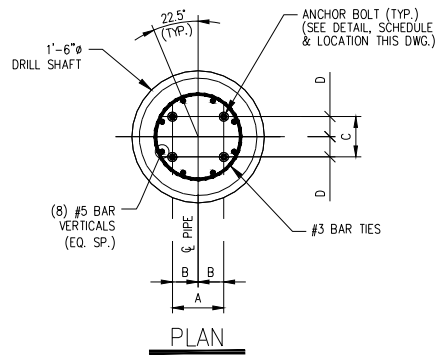


PIER SUPPORT DETAIL
FOR E-Z LINE SUPPORT 2" THRU 10"
(18 REQUIRED)

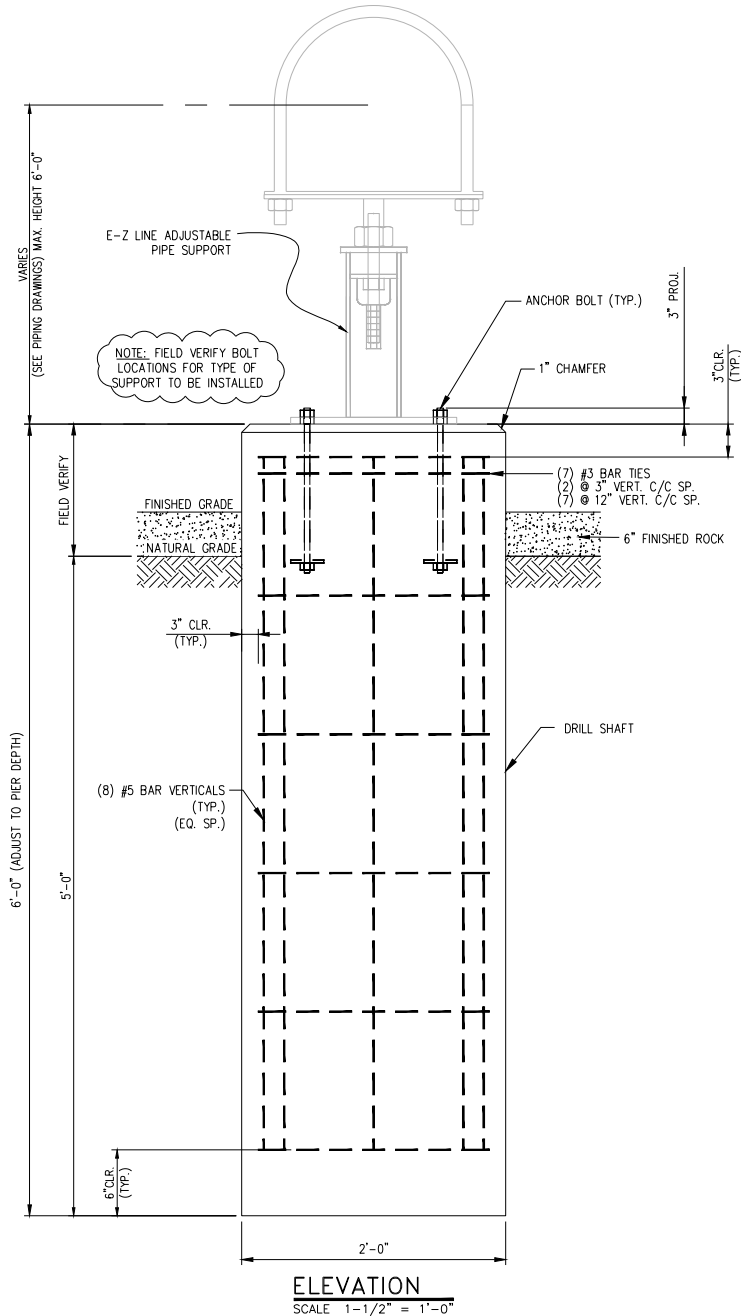

PIER SUPPORT DETAIL
FOR EZ LINE SUPPORT 12" THRU 24"
(1 REQUIRED)

NOTES:

1. CONCRETE CONSTRUCTION, MATERIALS AND TESTING SHALL BE IN ACCORDANCE WITH COMPANY STANDARDS.
2. CONCRETE PER ASTM C-94, 4000 PSI MINIMUM @ 28 DAYS.
3. REINFORCING STEEL TO BE ASTM A-615, DEFORMED BARS GRADE 60.
4. ALL EXPOSED CONCRETE EDGES SHALL HAVE A 1"x45' CHAMFER.
5. ANY EXCESS CONCRETE OR CHUTE CLEAN UP SHALL BE DEPOSITED AT A SITE DESIGNATED BY THE COMPANY REPRESENTATIVE. COUNTY ROADS OR BORROW DITCHES SHALL NOT BE USED FOR THIS PURPOSE.
6. ANY NEW CONCRETE SHALL HAVE FULL 7 DAYS OF CURE TIME PRIOR TO RECEIVING ANY LOADING UNLESS AUTHORIZED BY THE FIELD ENGINEER.
7. GROUTING TO BE FIVE STAR "NON-SHRINK" EPOXY GROUT (OR EQUAL) OR FIVE STAR "NON-SHRINK" CEMENT GROUT (OR EQUAL). ROUGHEN SURFACE PRIOR TO GROUT PLACEMENT.
8. PRE-INSTALLED ANCHOR BOLTS CAN BE REPLACED BY FIELD INSTALLED ANCHOR BOLTS PROVIDED OR SPECIFIED BY EZ-LINE WITH PROPER SIZE, EMBEDMENT AND PROJECTION.
9. EZ-LINE PIPE SUPPORT CAN BE REPLACED BY CUSTOM BUILT PIPE SUPPORT.

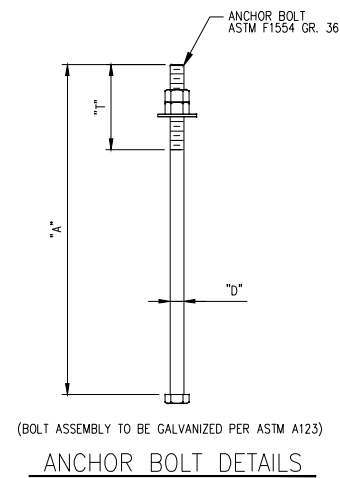

ANCHOR BOLT SCHEDULE						
PIPE SIZE	QTY*	D	A	T	NUTS/BOLT	REMARKS
2" THRU 10"	4	1/2"	1'-0"	4"	(2)H.H. NUTS	(1)FL. WSHR.
12" THRU 18"	4	5/8"	1'-3"	4"	(2)H.H. NUTS	(1)FL. WSHR.
20" THRU 24"	4	3/4"	1'-3"	4"	(2)H.H. NUTS	(1)FL. WSHR.
30" THRU 36"	4	3/4"	1'-3"	4"	(2)H.H. NUTS	(1)FL. WSHR.

* QUANTITY FOR EACH SUPPORT

ANCHOR BOLT SPACING CHART				
PIPE SIZE	A	B	C	D
2" THRU 4"	5"	2 1/2"	3 1/2"	1 3/4"
5" THRU 10"	7"	3 1/2"	5 1/2"	2 3/4"
12" THRU 24"	9"	4 1/2"	7 1/2"	3 3/4"
30" THRU 36"	11"	5 1/2"	9 1/2"	4 3/4"

**ISSUED FOR
CONSTRUCTION**
02/01/24



CHK STATELINE PIPELINE
SADDLER WELL PAD RISER
CONC. PEDESTAL PIPE SUPPORTS

PANOLA COUNTY, TEXAS





WBS NO.	
OLD DRAWING NO.	-
DRAWING NO.	13932M100
REV. NO.	0

NOTE:

1. CONTRACTOR TO FIELD VERIFY ALL DIMENSIONS AND ELEVATIONS.

REFERENCE DRAWINGS								FACILITY CODE	
								OR ACCOUNT NO:	
								CONSTRUCTION YEAR: 2023	
								BY	DATE
								DRAWN	AT 01/11/24
								CHECK	JM 01/11/24
								APPROVED	JM 01/11/24
0	ISSUED FOR CONSTRUCTION			AT	02/01/24	ZR	JM		
REV	DESCRIPTION			BY	DATE	CHK'D	APP'D	SCALE: 3/4"=1'-0"	

BILL OF MATERIAL - MAINLINE RISER 1 PIPE FENCE			
MARK	SIZE	QUANTITY	DESCRIPTION
1	3"	100'-0"	PIPE, 0.216" WT, ERW/SMLS, ASTM A106, GR. B
2	3"	8	CAP, BW, 0.216" WT, ASTM A234, WPB

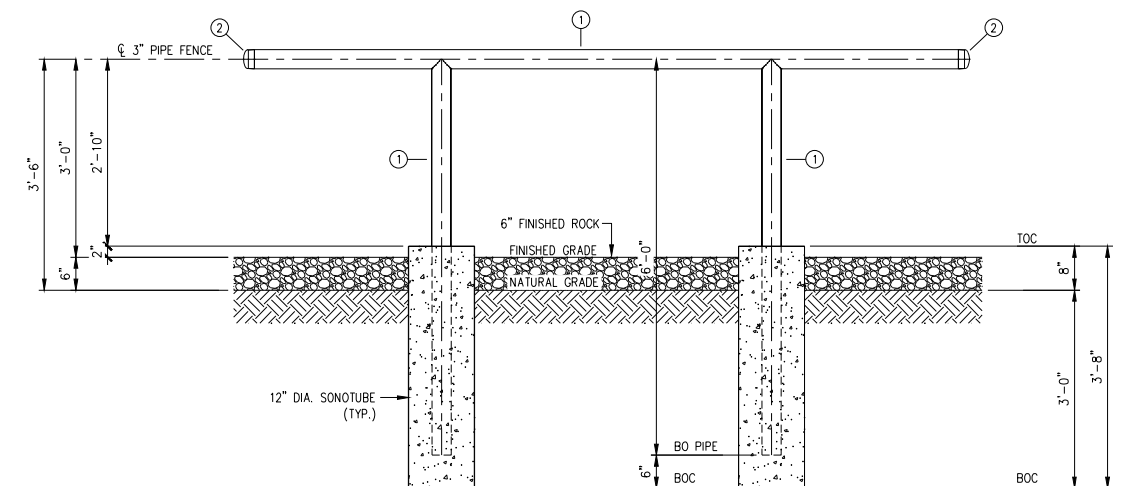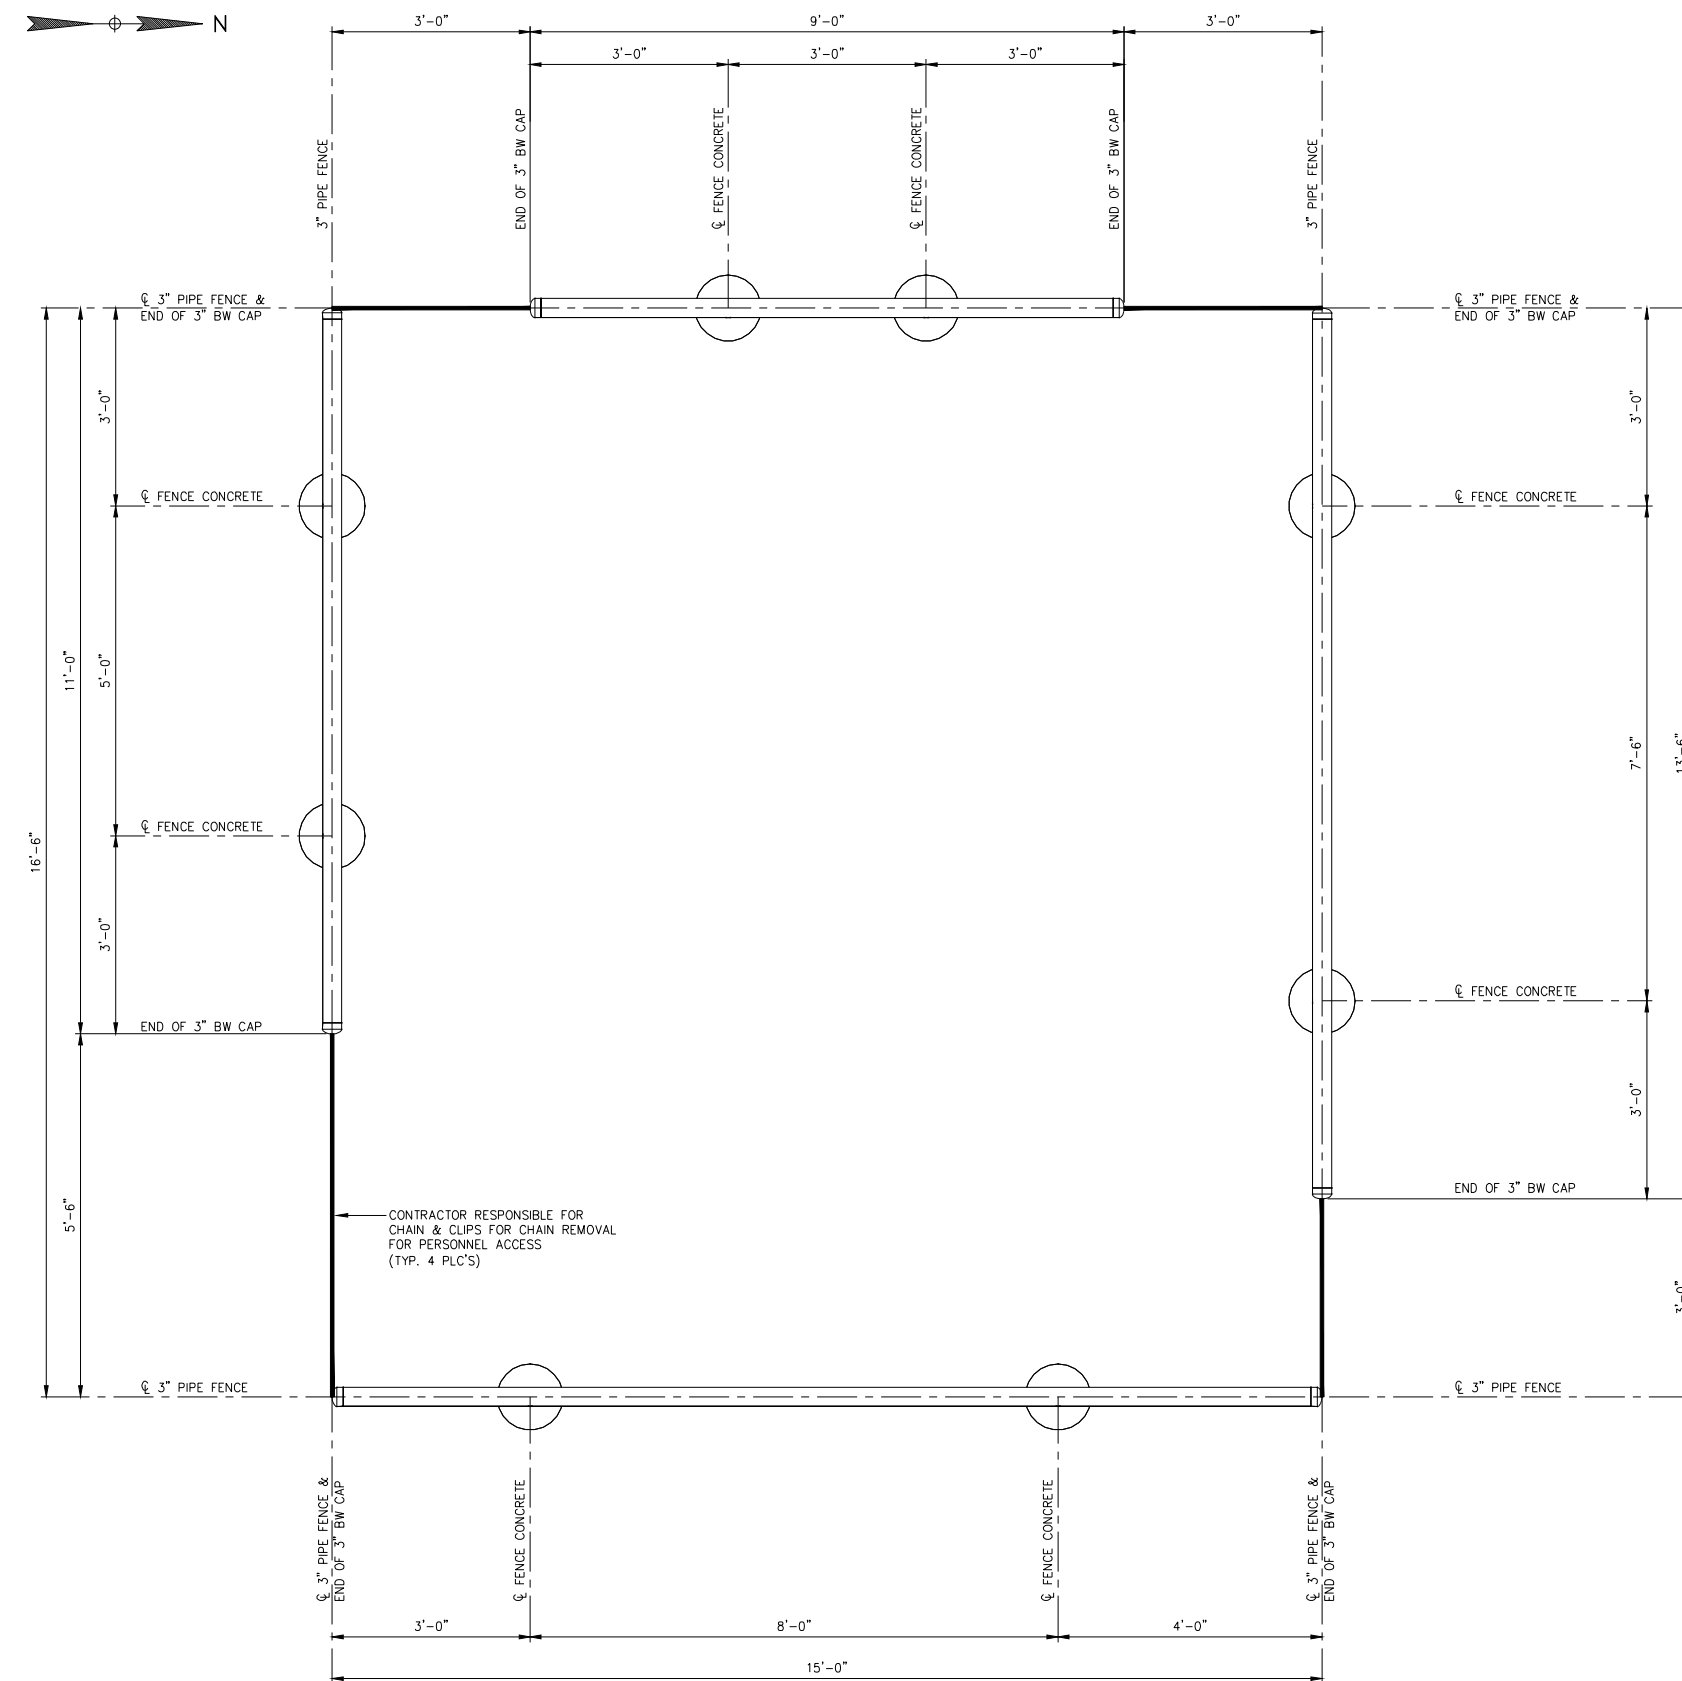



TYPICAL PIPE FENCE ELEVATION

NOTE:

1. CONTRACTOR TO FIELD VERIFY ALL DIMENSIONS AND ELEVATIONS.

REFERENCE DRAWINGS													CHK STATELINE PIPELINE MAINLINE RISER 1 PIPE FENCE DETAILS PLAN, ELEVATION & BOM	WBS NO.	
														OLD DRAWING NO.	
														—	
	0	ISSUED FOR CONSTRUCTION			AT	02/01/24	ZR	JM						DRAWING NO.	REV. NO.
REV		DESCRIPTION			BY	DATE	CHK'D	APP'D	SCALE: 3/4"=1'-0"				13932M101	0	

BILL OF MATERIAL - CHK/NG RISER PIPE FENCE			
MARK	SIZE	QUANTITY	DESCRIPTION
1	3"	100'-0"	PIPE, 0.216" WT, ERW/SMLS, ASTM A106, GR. B
2	3"	8	CAP, BW, 0.216" WT, ASTM A234, WPB

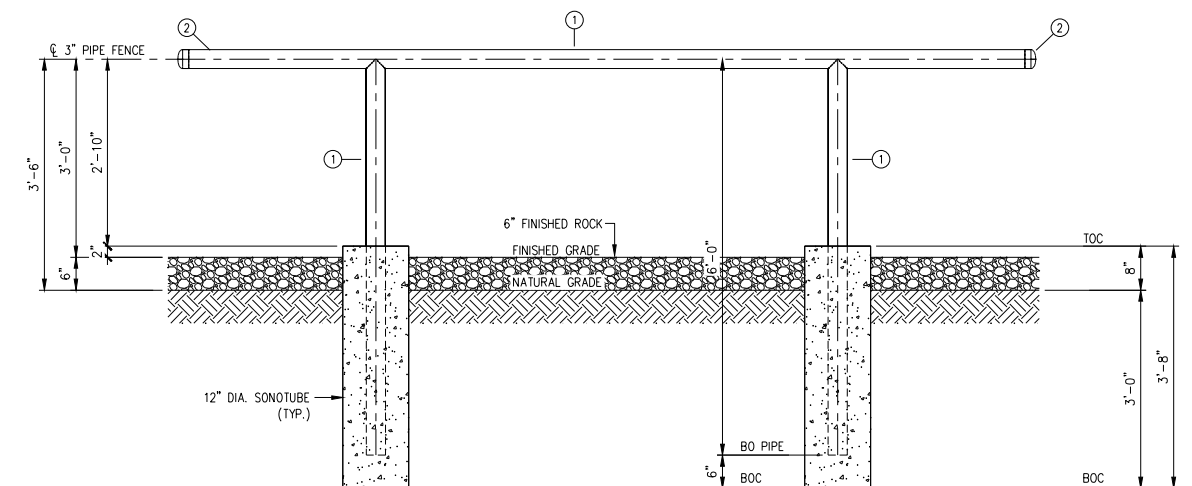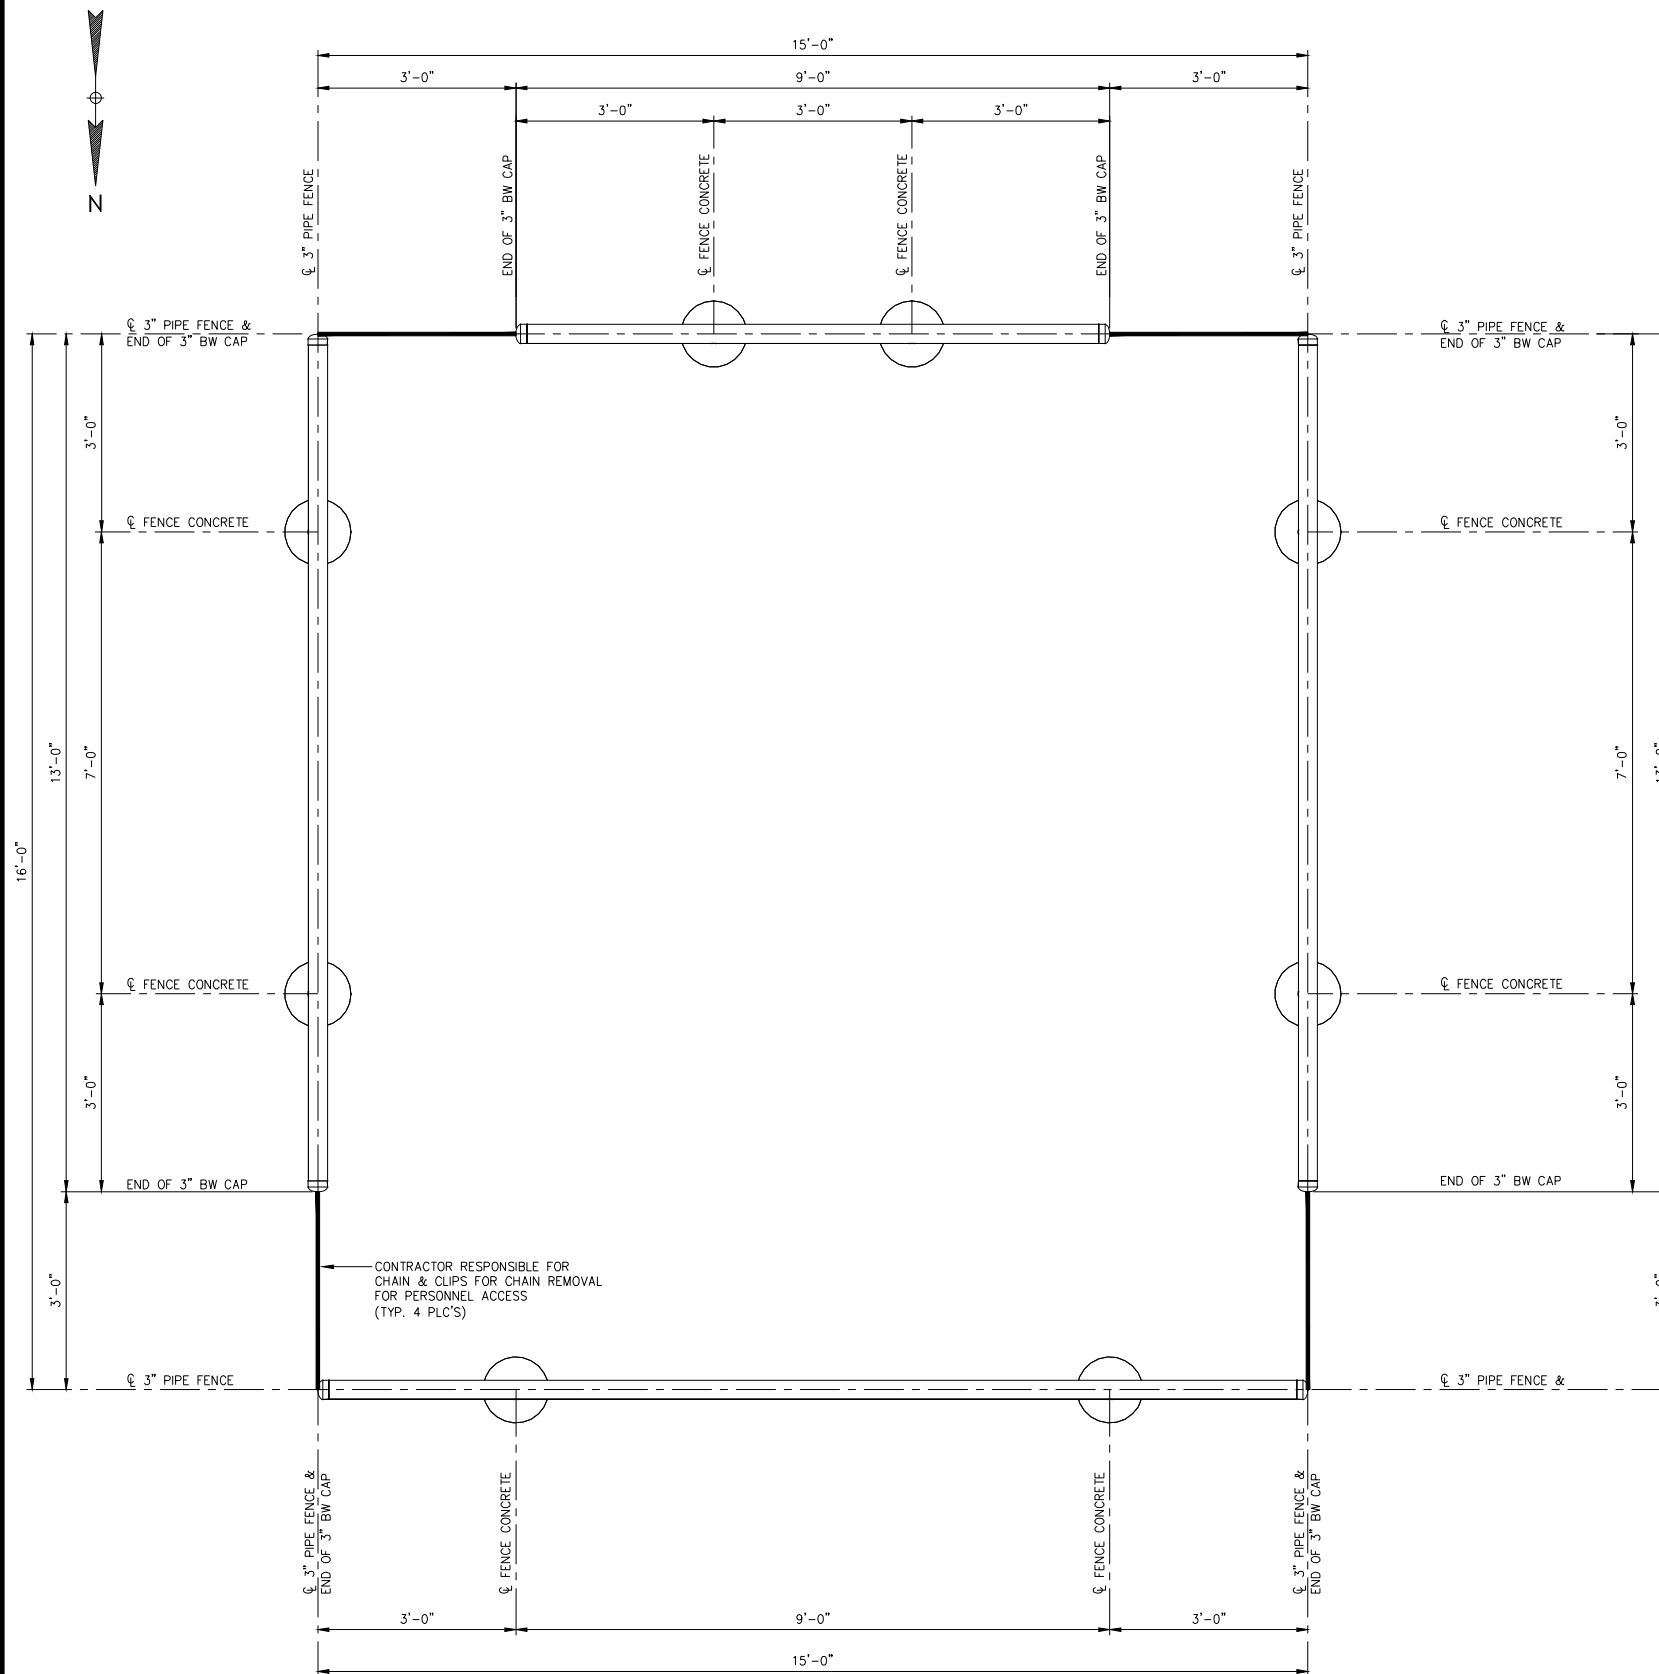



TYPICAL PIPE FENCE ELEVATION

NOTE:

1. CONTRACTOR TO FIELD VERIFY ALL DIMENSIONS AND ELEVATIONS.

REFERENCE DRAWINGS								FACILITY CODE OR ACCOUNT NO:				CHK STATELINE PIPELINE CHK/NG RISER PIPE FENCE DETAILS PLAN, ELEVATION & BOM	WBS NO.			
								CONSTRUCTION YEAR: 2024					OLD DRAWING NO.			
								DRAWN BY DATE AT 01/11/24					-			
								CHECK JM 01/11/24								
								APPROVED JM 01/11/24								
0 ISSUED FOR CONSTRUCTION		AT		02/01/24		ZR		JM					DRAWING NO.		REV. NO.	
REV DESCRIPTION		BY		DATE		CHK'D		APP'D		SCALE: 3/4"=1'-0"			13932M102		0	

BILL OF MATERIAL - MAINLINE RISER 2 PIPE FENCE			
MARK	SIZE	QUANTITY	DESCRIPTION
1	3"	100'-0"	PIPE, 0.216" WT, ERW/SMLS, ASTM A106, GR. B
2	3"	8	CAP, BW, 0.216" WT, ASTM A234, WPB

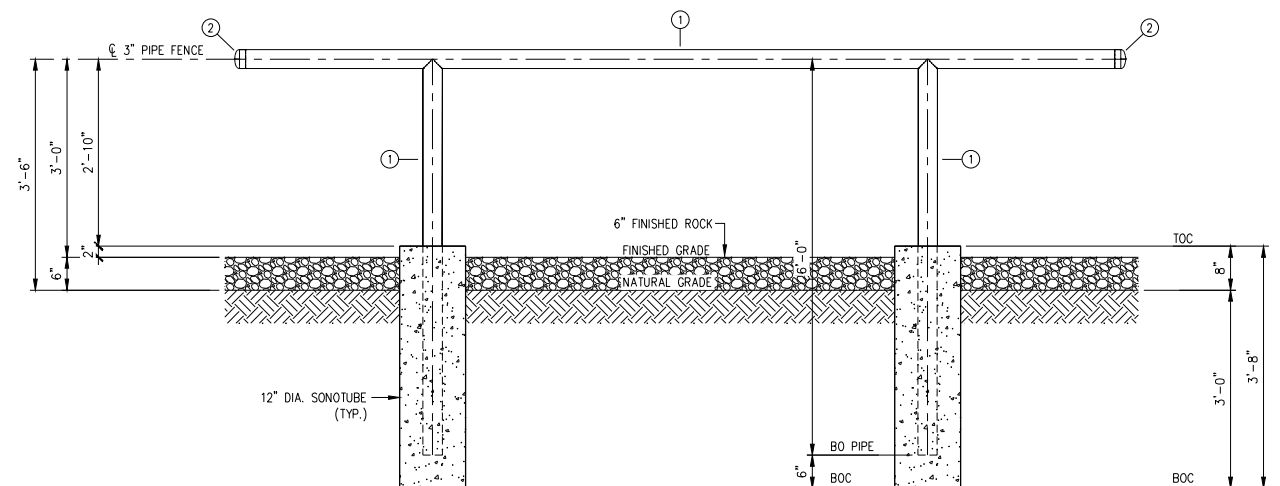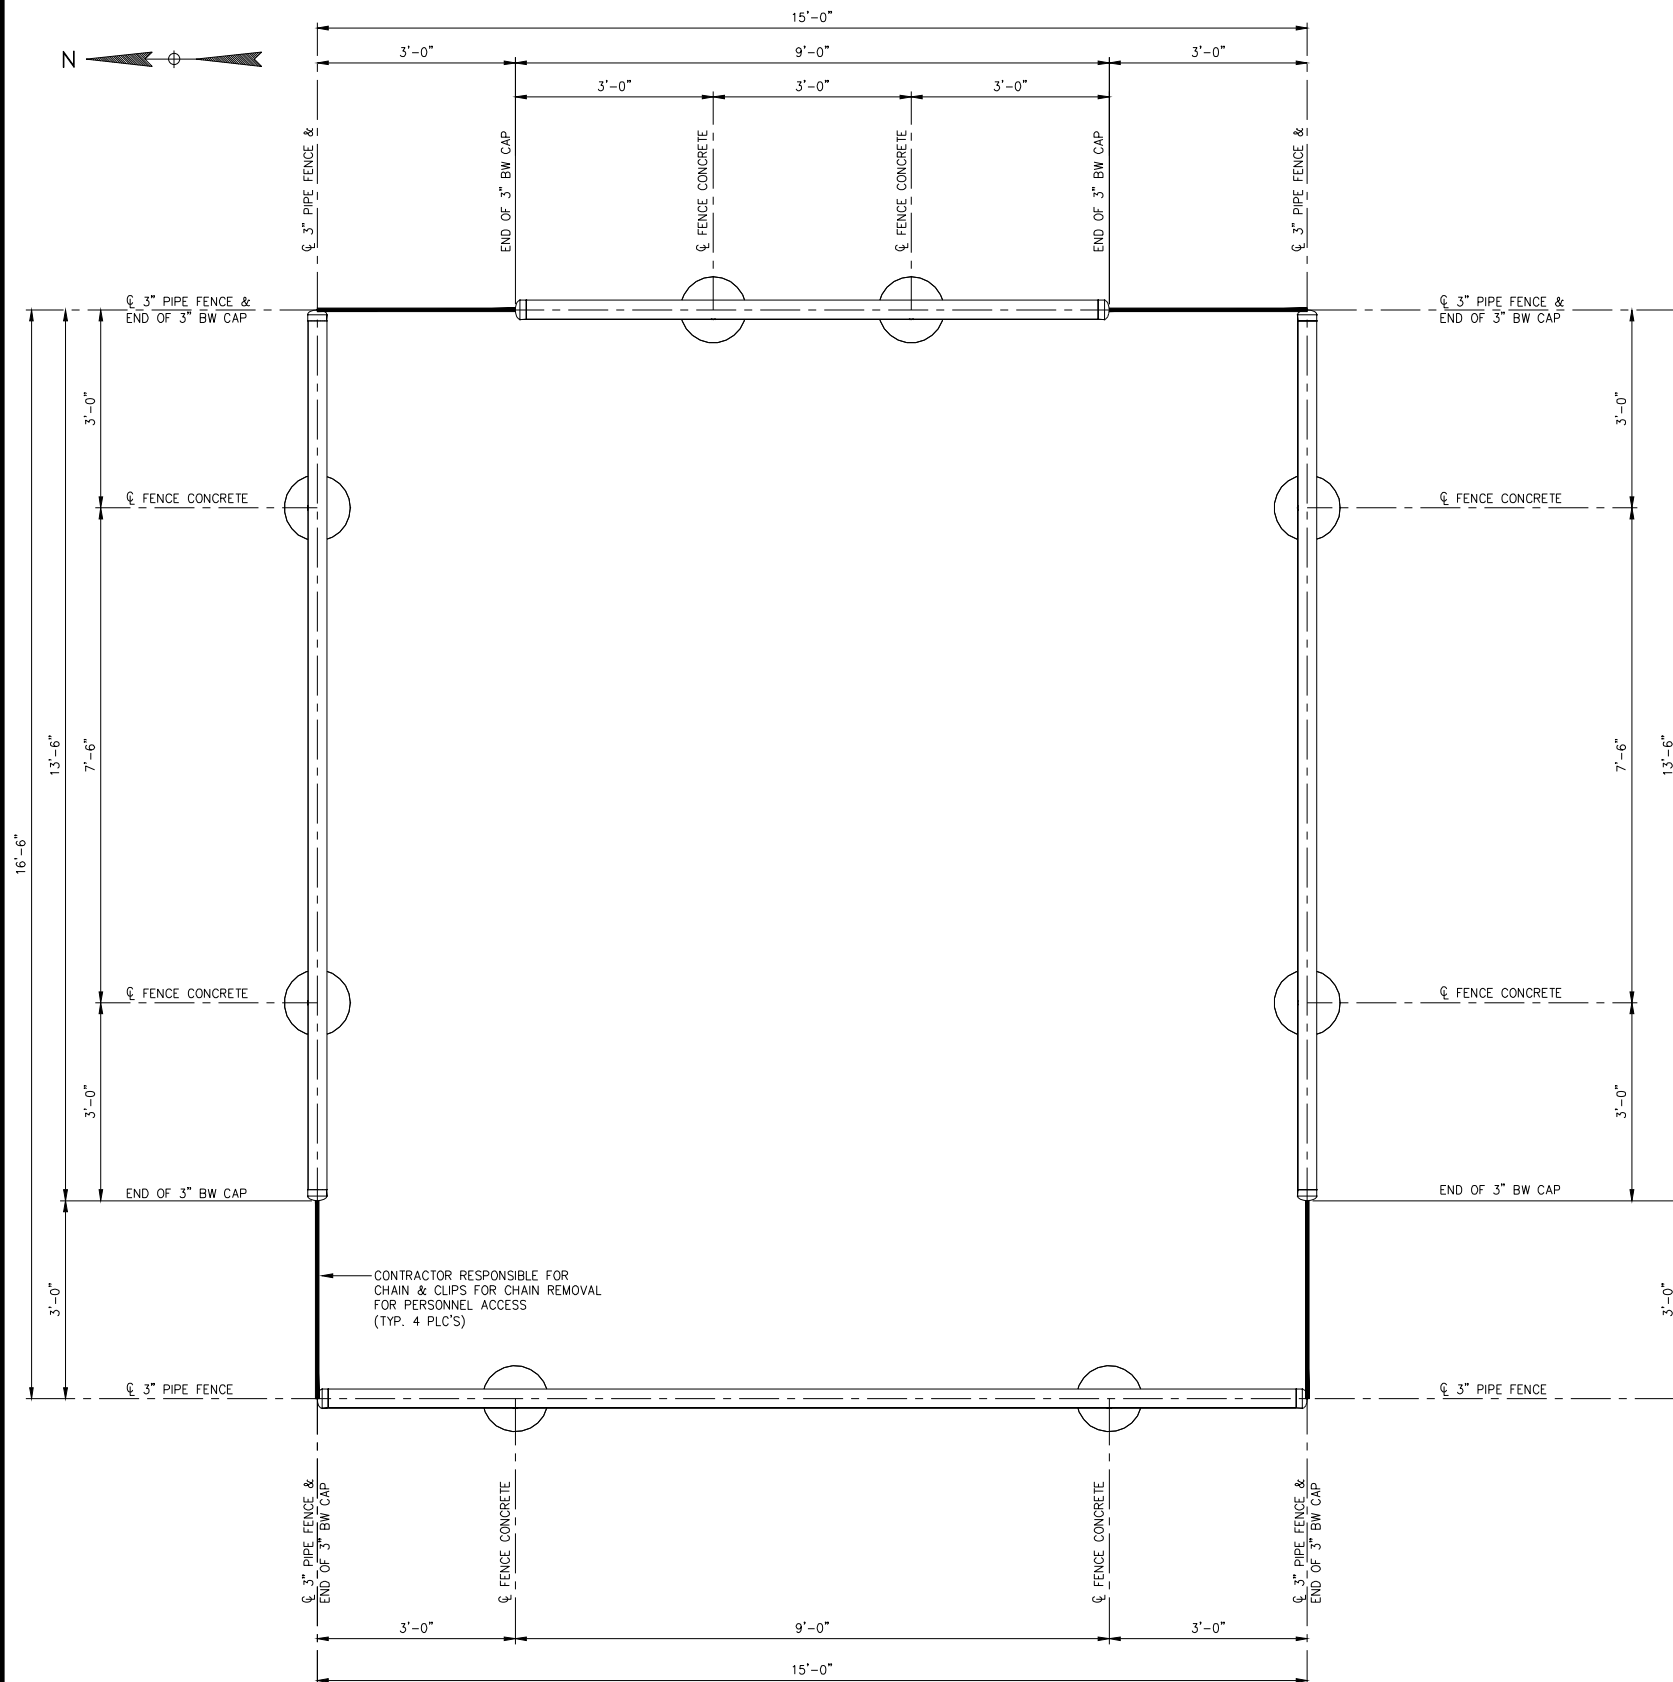

TYPICAL PIPE FENCE ELEVATION

NOTE:

1. CONTRACTOR TO FIELD VERIFY ALL DIMENSIONS AND ELEVATIONS.

REFERENCE DRAWINGS				FACILITY CODE OR ACCOUNT NO.: CONSTRUCTION YEAR: 2024					CHK STATELINE PIPELINE MAINLINE RISER 2 PIPE FENCE DETAILS PLAN, ELEVATION & BOM	WBS NO.	
				DRAWN BY DATE AT 01/11/24						OLD DRAWING NO.	
				CHECK JM 01/11/24						-	
0 ISSUED FOR CONSTRUCTION				AT 02/01/24 ZR JM						DRAWING NO.	
REV DESCRIPTION				BY DATE CHK'D APP'D				SCALE: 3/4"=1'-0"		REV. NO.	
								13932M103		0	

